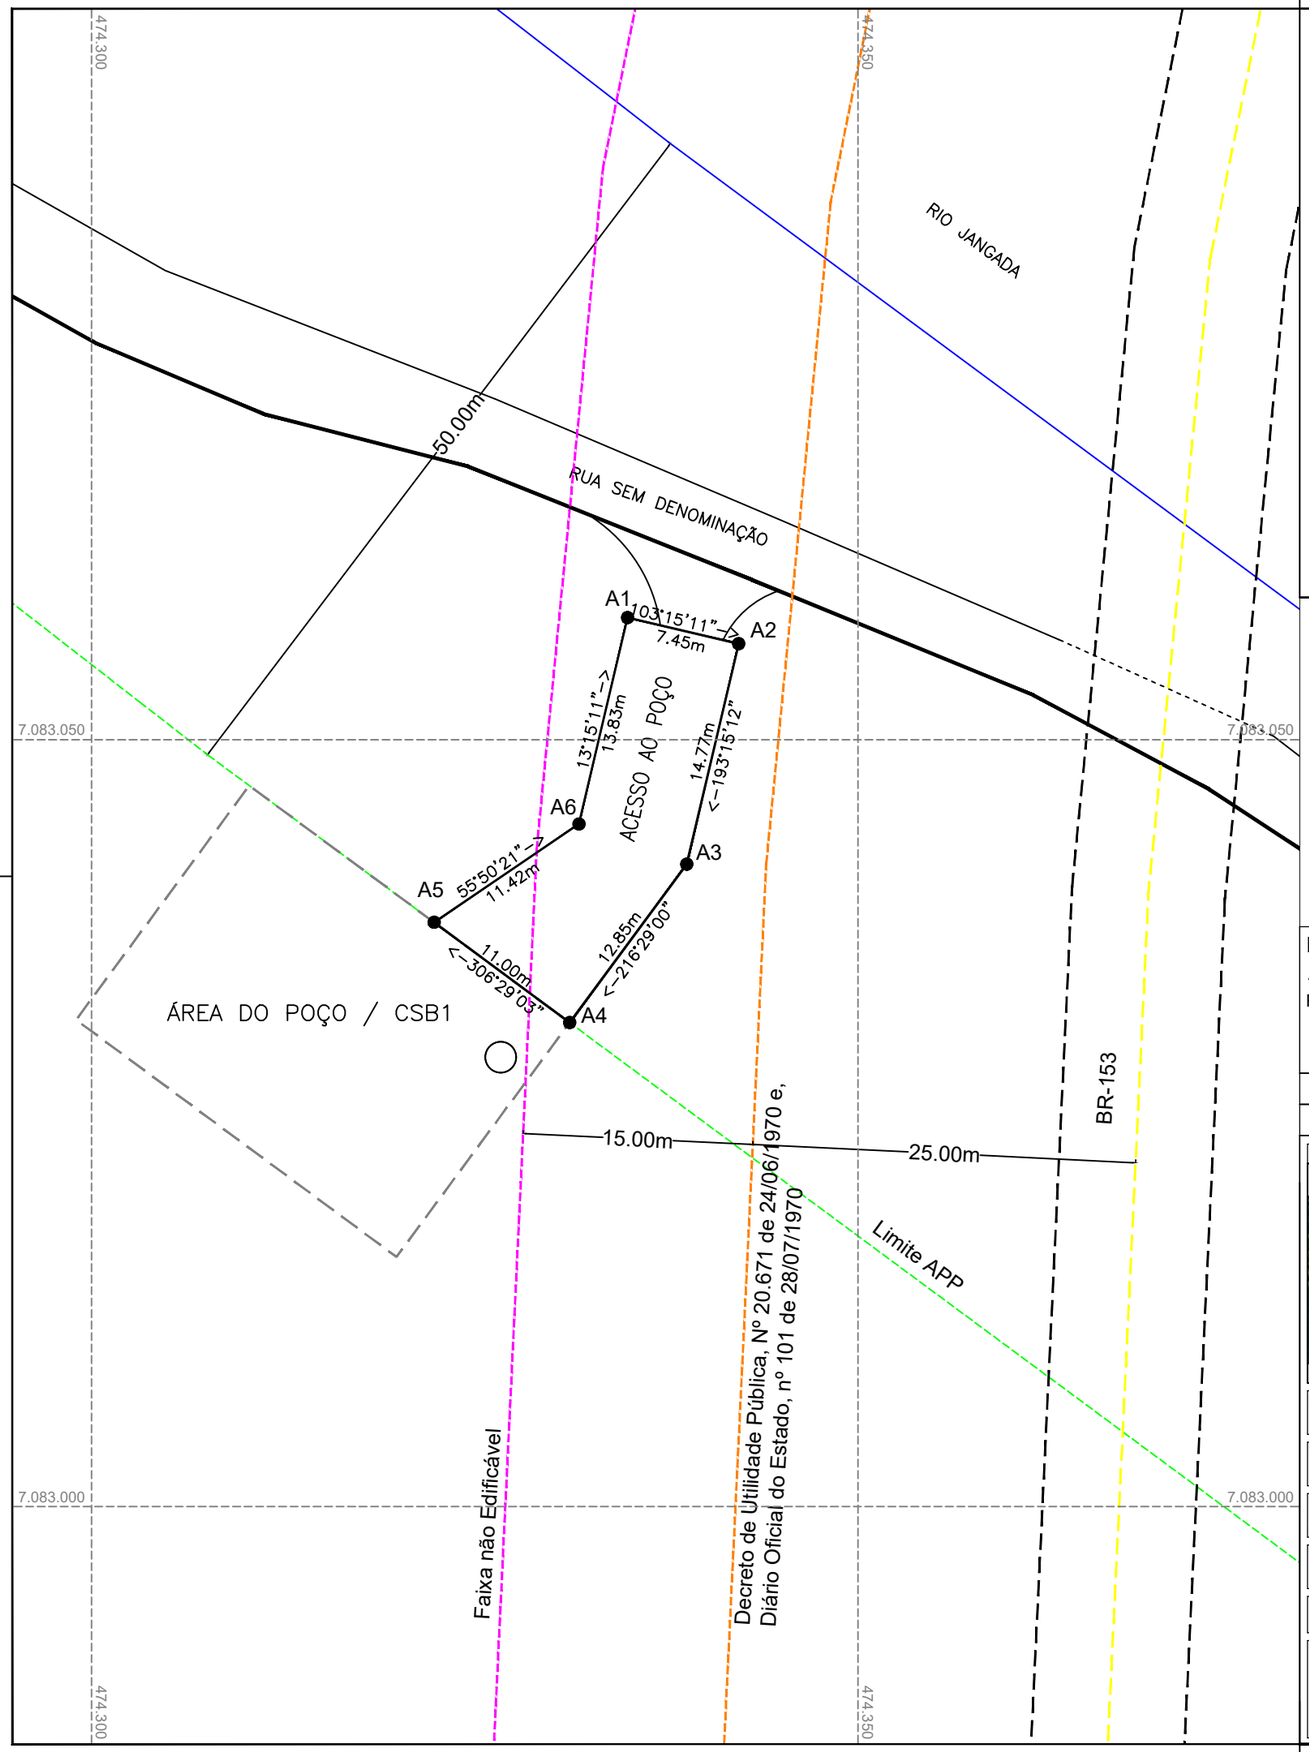
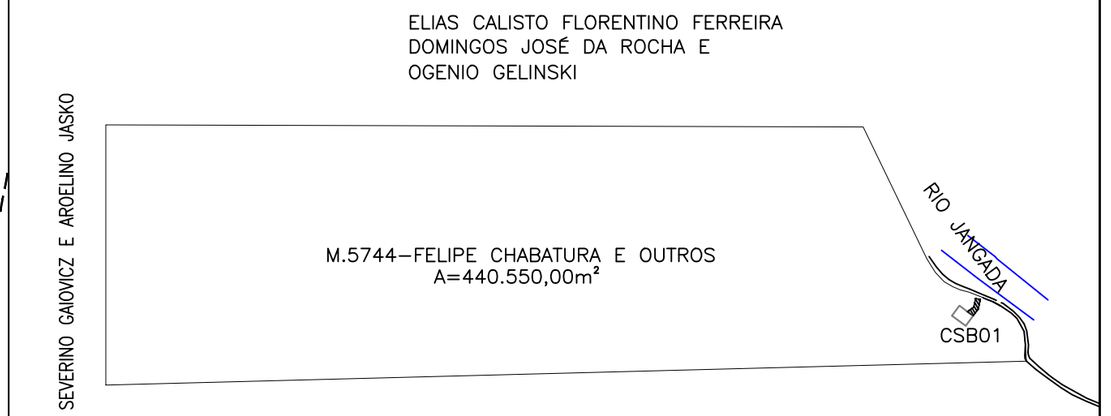


LOCALIZAÇÃO DO IMÓVEL



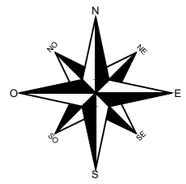


TABELA DE COORDENADAS - ACESSO					
LADOS		AZIMUTE	DIST. (m)	COORD. E (m)	COORD. N (m)
A1	A2	103°15'11"	7,45	474334,955	7083057,963
A2	A3	193°15'12"	14,77	474342,206	7083056,255
A3	A4	216°29'00"	12,85	474338,820	7083041,878
A4	A5	306°29'03"	11,00	474331,182	7083031,549
A5	A6	55°50'21"	11,42	474322,338	7083038,090
A6	A1	13°15'11"	13,83	474331,784	7083044,500

INFORMAÇÕES TÉCNICAS

ÁREA DE ATINGIMENTO (ACESSO):	212,13 m²
PERÍMETRO (ACESSO):	71,32 m


Nº	DESCRIÇÃO DA REVISÃO	DATA	ADEQUAÇÃO	RESP. TÉCNICO

LOCALIZAÇÃO DO IMÓVEL



CONVENÇÕES CARTOGRAFICAS

- VÉRTICES
- LIMITE EM LINHA SECA
- RODOVIA
- LIMITE DA APP
- FAIXA DE DOMÍNIO
- FAIXA NÃO EDIFICÁVEL

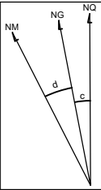

COORDENADAS PLANAS SISTEMA UTM
DATUM: SIRGAS2000
DATUM VERTICAL: IMBITUBA / SC
PONTO: A1
LATITUDE: 25°49'49.4"S
LONGITUDE: 52°44'00.7"W — MERIDIANO CENTRAL: 51 WGr
DATA: 22/05/2022 — COEFICIENTE DE ESCALA K: 1,00045437016
CONVERGENCIA MERIDIANA (c): 1° 05' 43.0"
DECLINAÇÃO MAGNÉTICA (d): 18°09' W — VAR. ANUAL: 0°16' W

Folha 01/01

PROJETO / UNIDADE CONSTRUTIVA
LEGALIZAÇÃO DA FAIXA DE SERVIDÃO DE ACESSO À ÁREA DO POÇO CSB01

IMÓVEL
ÁREA DE TERRAS MEDINDO 440.550,00m²

ESCALA
1 / 400

EXECUTANTE
Sociedade da Água
Serviços Ambientais e Engenharia
Desde 1995

DETENTOR
FELIPE CHABATURA E OUTROS
OU A QUEM DE DIREITO PERTENCER

ART
1720231599408

MUNICÍPIO/UF
GENERAL CARNEIRO / PR

COMARCA
JANGADA DO SUL / PR

DATA
SETEMBRO / 2023

RESPONSÁVEL TÉCNICO
PAULO CEZAR TOSIN:32072597900
Assinado de forma digital por PAULO CEZAR TOSIN:32072597900
Dados: 2023.09.29 08:53:06 -03'00'
Paulo Cezar Tosin
Paulo Cezar Tosin CREA Nº 11.534-D/PR

CÓDIGO DO IMÓVEL
INCRA 724.041.003.778-1

CERTIDÃO DE REGISTRO
MAT.5744-1º CRI UNIÃO DA VITÓRIA

COORD. GERAL DO PROJETO
DENIS SCHECHTEL NEVES - CRQ: 09402617/PR

ARQUIVO ELETRÔNICO
001-SAA-0674-0000-LEGA-DE-0000CSB01JANGADA-R0

MEMORIAL DESCRITIVO
001-SAA-0674-0000-LEGA-MD-0000CSB01JANGADA-R0

SANEPAR
COMPANHIA DE SANEAMENTO DO PARANÁ

UNIDADE SANEPAR
GPOSD
GERÊNCIA PROJETOS E OBRAS SUDOESTE
Rua Monte Alverne nº644 - Jardim Carvalho - CEP 84016-010 - Ponta Grossa-PR
GERENTE: JOEL PIRES — CREA Nº: 100.276 - D/PR

CÓPIA CONFERE COM O ORIGINAL