

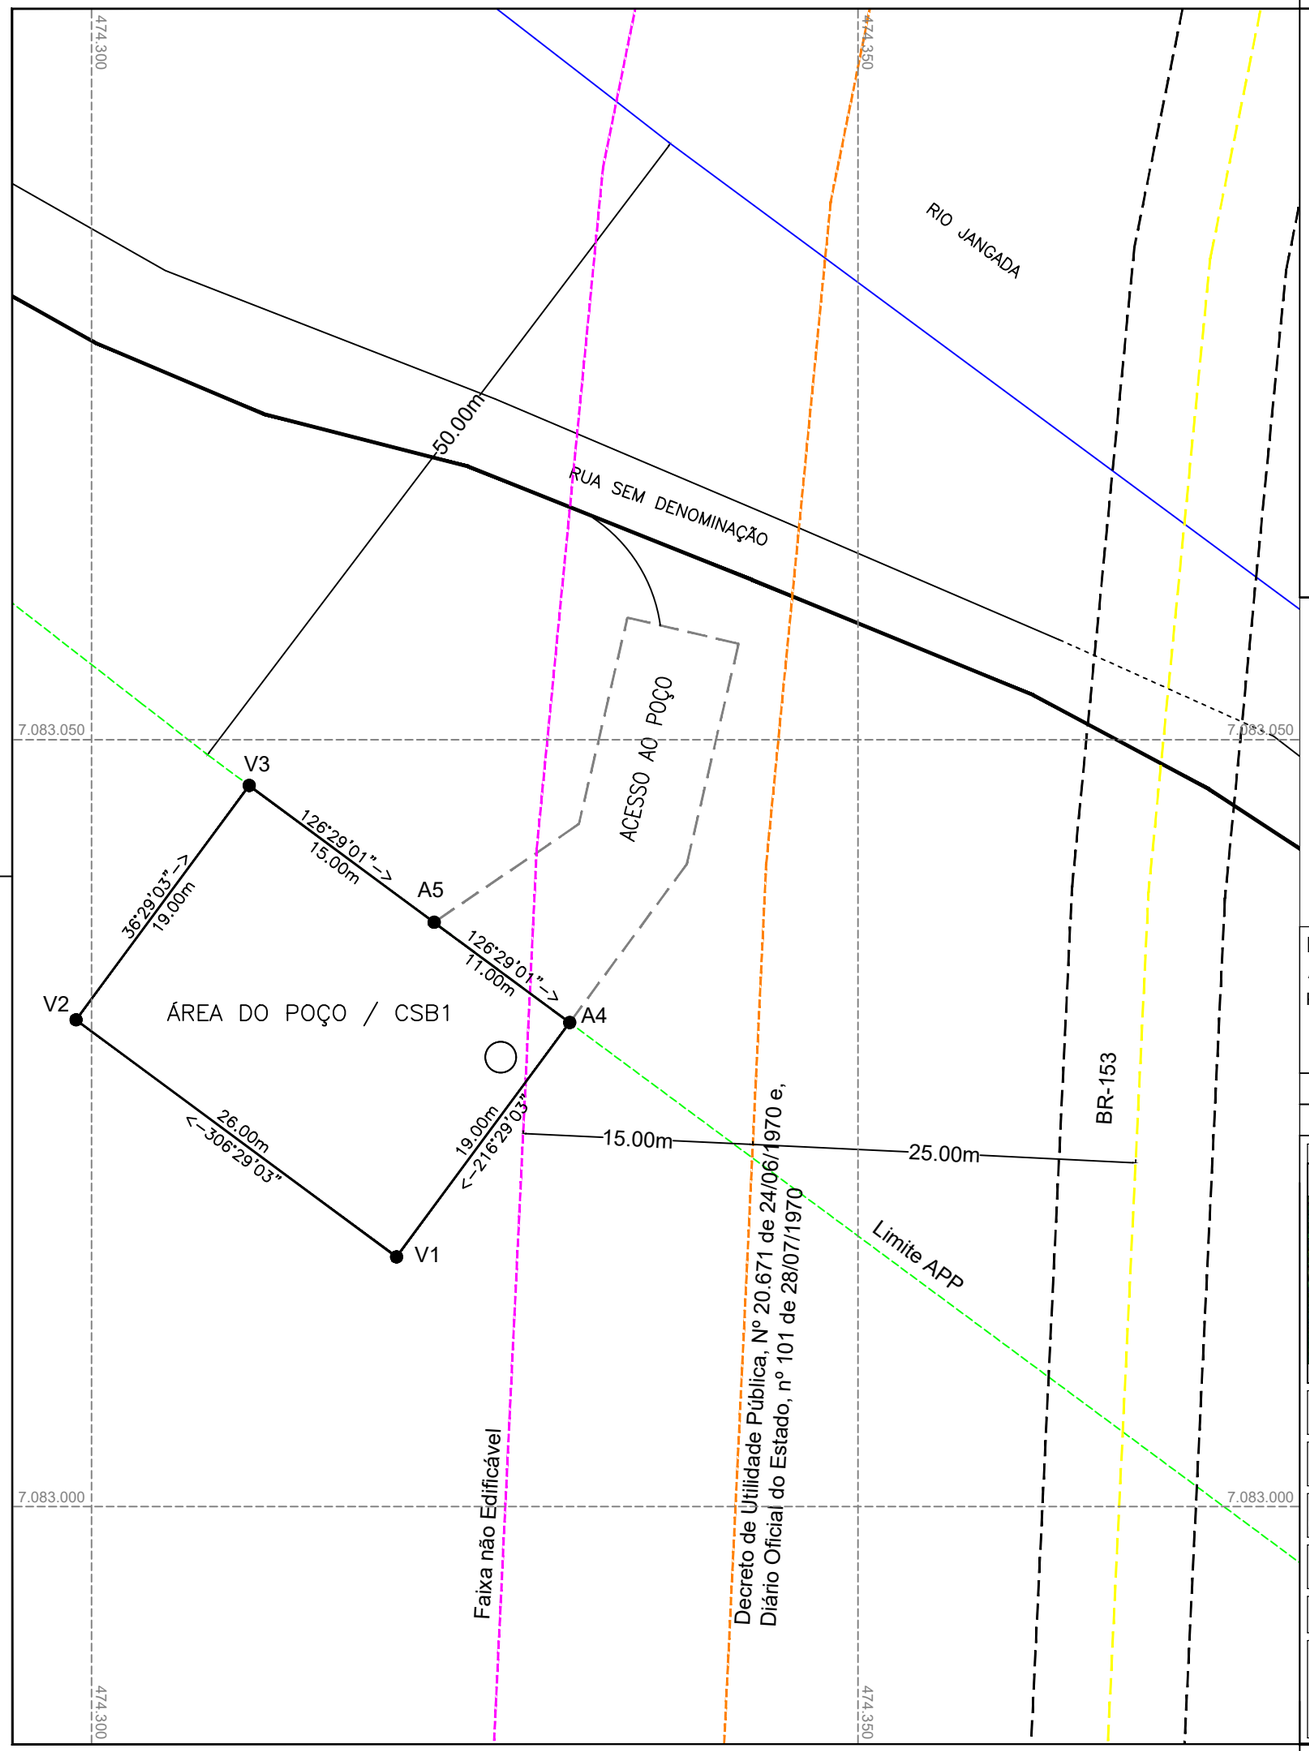


LOCALIZAÇÃO DO IMÓVEL

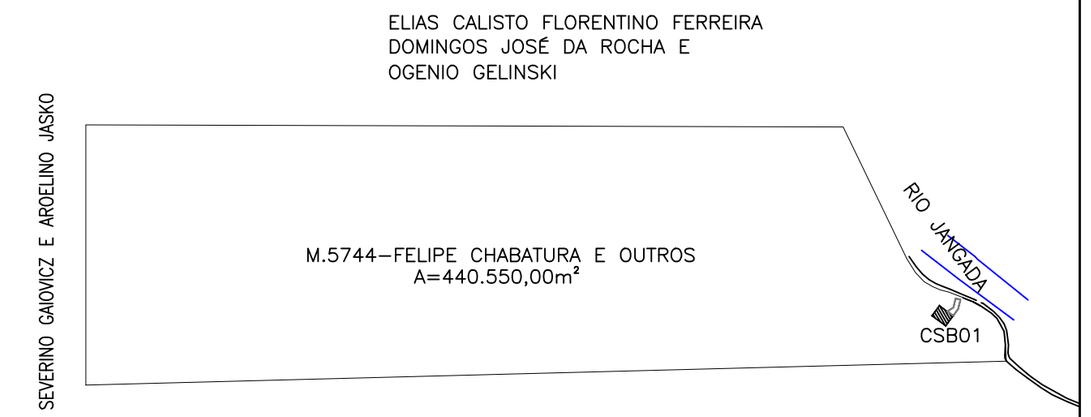

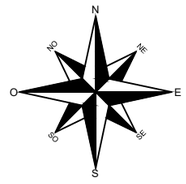

INFORMAÇÕES TÉCNICAS

ÁREA DE ATINGIMENTO (CSB01):	494,00 m²
PERÍMETRO (CSB01):	90,00 m

TABELA DE COORDENADAS - ÁREA CSB01

LADOS		AZIMUTE	DIST. (m)	COORD. E (m)	COORD. N (m)
A4	V1	216°29'03"	19,00	474331,182	7083031,549
V1	V2	306°29'03"	26,00	474319,885	7083016,273
V2	V3	36°29'03"	19,00	474298,980	7083031,732
V3	A5	126°29'03"	15,00	474310,278	7083047,009
A5	A4	126°29'03"	11,00	474322,338	7083038,090


Nº	DESCRIÇÃO DA REVISÃO	DATA	ADEQUAÇÃO	RESP. TÉCNICO

LOCALIZAÇÃO DO IMÓVEL



CONVENÇÕES CARTOGRAFICAS

- VÉRTICES
- LIMITE EM LINHA SECA
- RODOVIA
- LIMITE DA APP
- FAIXA DE DOMÍNIO
- FAIXA NÃO EDIFICÁVEL

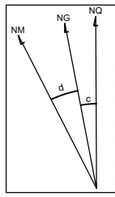

COORDENADAS PLANAS SISTEMA UTM

DATUM: SIRGAS2000
DATUM VERTICAL: IMBITUBA / SC
PONTO: V1
LATITUDE: 25°49'49.4"S
LONGITUDE: 52°44'00.7"W — MERIDIANO CENTRAL: 51 WGr
DATA: 22/05/2022 — COEFICIENTE DE ESCALA K: 1,00045437016
CONVERGENCIA MERIDIANA (c): 1º 05' 43.0"
DECLINAÇÃO MAGNÉTICA (d): 18°09' W — VAR. ANUAL: 0°16' W

Folha 01/01

PROJETO / UNIDADE CONSTRUTIVA
LEGALIZAÇÃO DA ÁREA DO POÇO CSB01

IMÓVEL
ÁREA DE TERRAS MEDINDO 440.550,00m²

ESCALA
1 / 400

EXECUTANTE
Sociedade da Água — Serviços Ambientais e Engenharia — Desde 1998

DETENTOR
FELIPE CHABATURA E OUTROS
OU A QUEM DE DIREITO PERTENCER

ART
1720231599408

MUNICÍPIO/UF
GENERAL CARNEIRO / PR

COMARCA
JANGADA DO SUL / PR

DATA
SETEMBRO / 2023

RESPONSÁVEL TÉCNICO
PAULO CEZAR TOSIN:32072597900
Assinado de forma digital por PAULO CEZAR TOSIN:32072597900 Dados: 2023.09.29 08:53:59 -03'00'
Paulo Cezar Tosin
Paulo Cezar Tosin CREA Nº 11.534-D/PR

CÓDIGO DO IMÓVEL
INCRA 724.041.003.778-1

CERTIDÃO DE REGISTRO
MAT.5744-1º CRI UNIÃO DA VITÓRIA

COORD. GERAL DO PROJETO
DENIS SCHECHTEL NEVES - CRQ: 09402617/PR

ARQUIVO ELETRÔNICO
002-SAA-0674-0000-LEGA-DE-0000CSB01JANGADA-R0

MEMORIAL DESCRITIVO
002-SAA-0674-0000-LEGA-MD-0000CSB01JANGADA-R0

SANEPAR
COMPANHIA DE SANEAMENTO DO PARANÁ

UNIDADE SANEPAR
GPOSD
GERÊNCIA PROJETOS E OBRAS SUDOESTE
Rua Monte Alverne nº644 - Jardim Carvalho - CEP 84016-010 - Ponta Grossa-PR
GERENTE: JOEL PIRES — CREA Nº: 100.276 - D/PR

CÓPIA CONFERE COM O ORIGINAL