
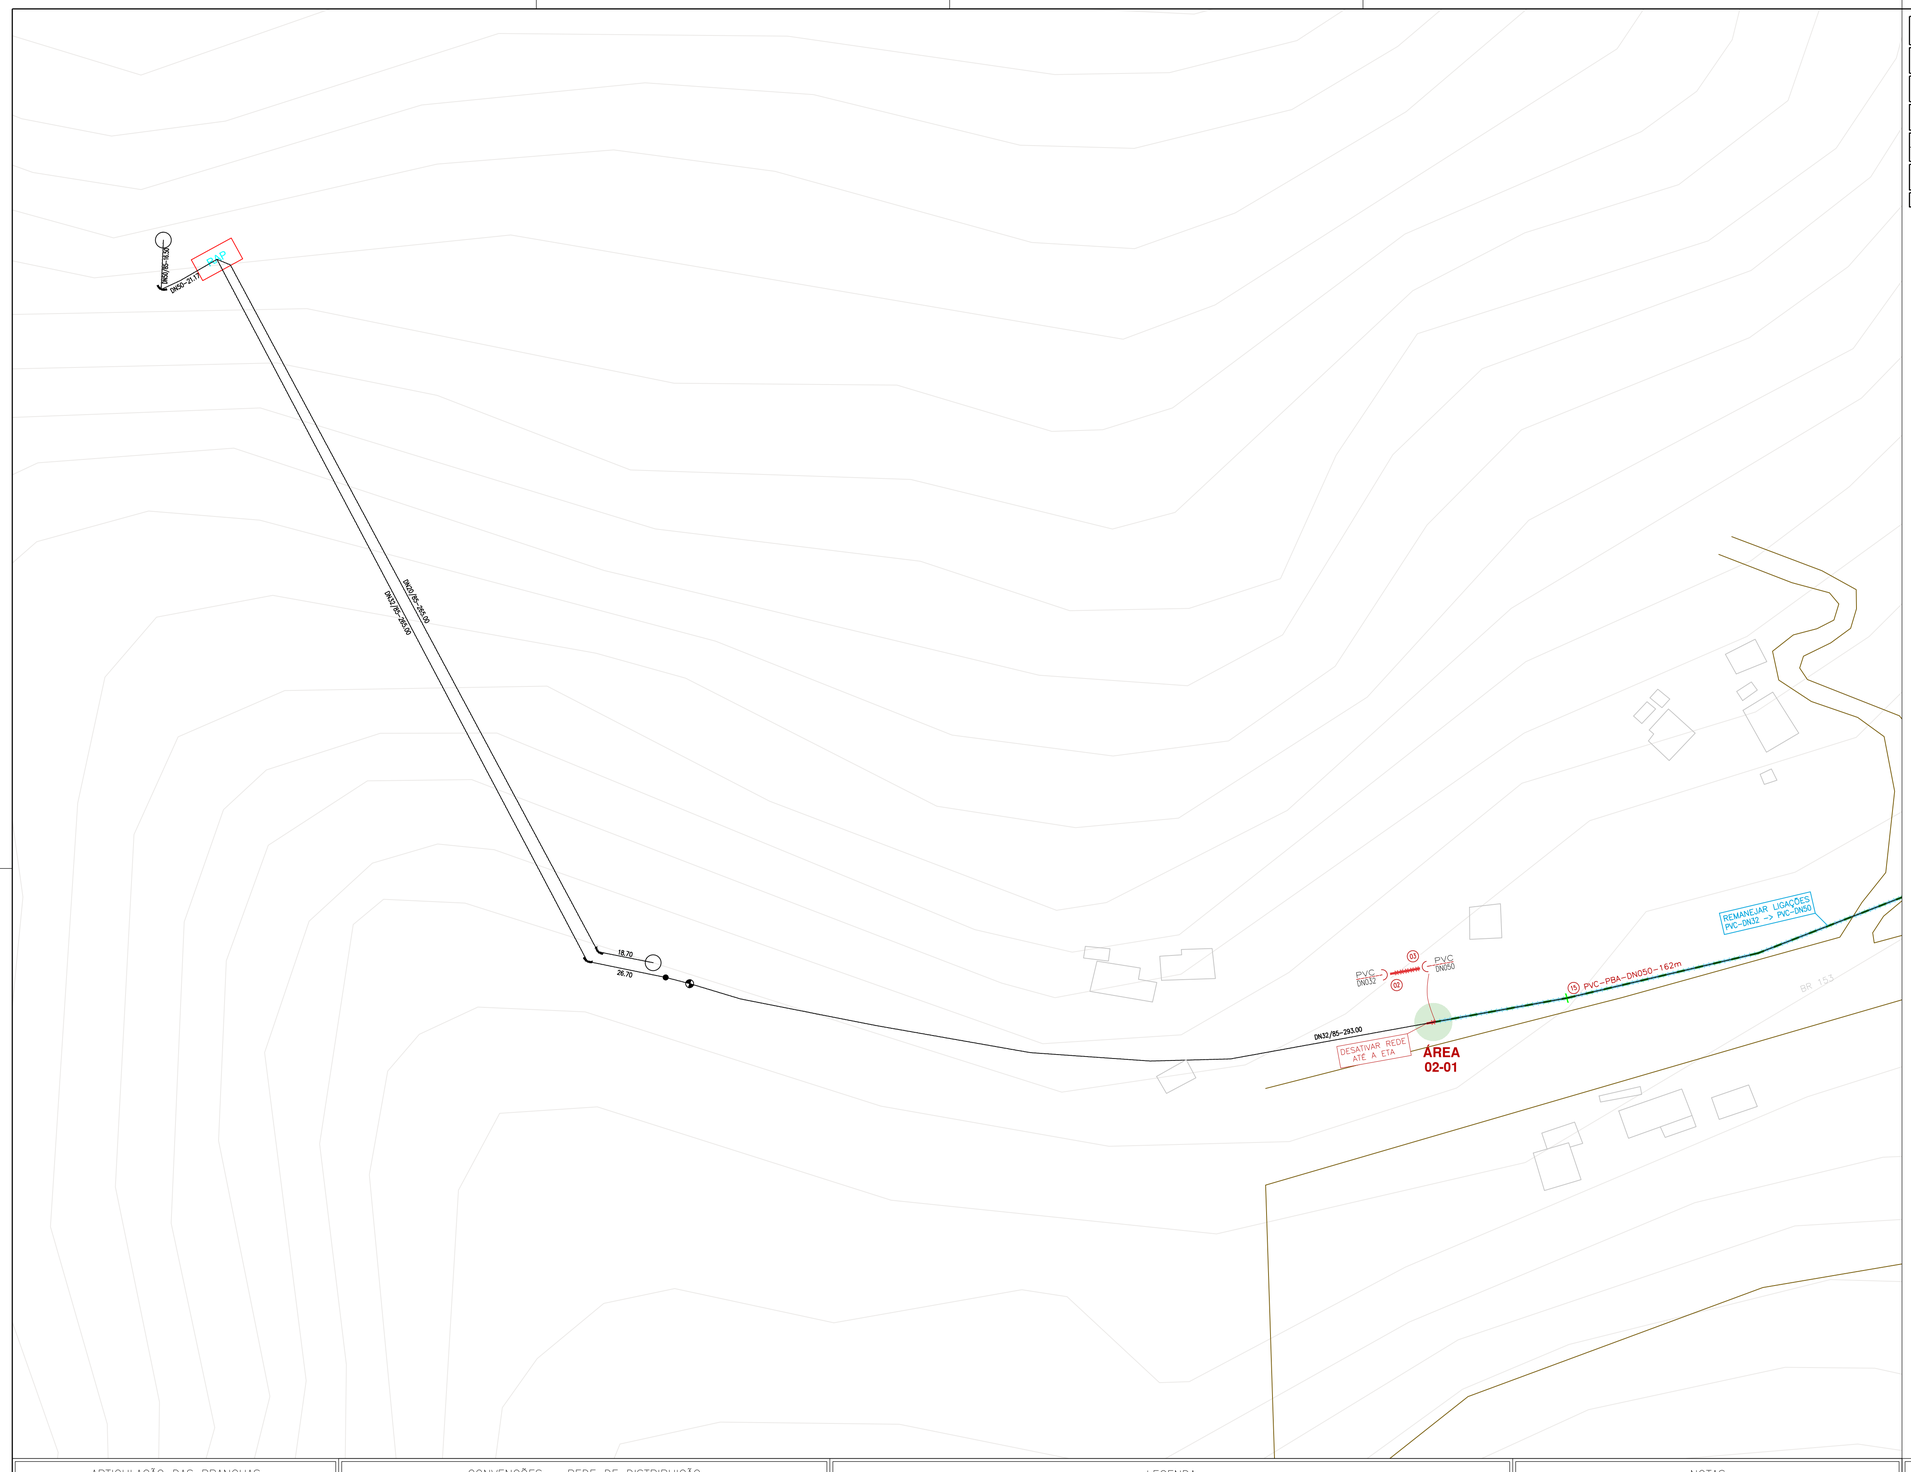


RELAÇÃO DE EQUIPAMENTOS E MATERIAIS

REDE DE DISTRIBUIÇÃO DE ÁGUA

COD.	Nº	DISCRIMINAÇÃO	QT.	UN.
		ÁREA-02-01		
323941	02	CAP PVC-U JS BB PN750KPA NBR 5648 DE 32	1	PÇ
20630	03	CAP PVC JE COM ANEL DN50	1	PÇ
		TUBULAÇÕES DA PRANCHA		
27570	15	TUBO PVC JEI PB PN 0,60 MPA - NBR 5647 (COMPRIMENTO TOTAL 6M UTIL 5,88M) DN50	162	m

ARTICULAÇÃO DAS PRANCHAS

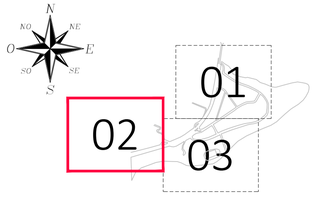

GENERAL CARNEIRO – JANGADA DO SUL

CONVENÇÕES – REDE DE DISTRIBUIÇÃO

- PVC PBA DN50
- PEAD DE90
- LIMITES DAS ZONAS DE PRESSÃO
- LIMITES DOS SETORES DE MANOBRA
- TUBULAÇÕES EXISTENTES
- TUBULAÇÕES VIRGENS
- REDE À DESATIVAR
- REDE À SUBSTITUIR
- HIDROGRAFIA

LEGENDA

- CAP
- CURVA 22 PB
- CURVA 45 PB
- CURVA 90 PB
- CURVA 11 BB
- CURVA 22 BB
- CURVA 45 BB
- CURVA 90 BB
- LUVA BB
- REDUÇÃO BB
- REDUÇÃO PB
- EXTREMIDADE FB
- EXTREMIDADE FP
- TRANSIÇÃO
- COLARINHO E FLANGE
- CRUZETA BBBB
- TÊ BBB
- TÊ DE REDUÇÃO BBB
- JUNÇÃO BBB
- HIDRANTE
- MACROMEDIDOR
- VENTOSA
- REGISTRO DE MANOBRA ABERTO – PROJETADO
- REGISTRO DE MANOBRA ABERTO – EXISTENTE
- REGISTRO DE MANOBRA FECHADO – PROJETADO
- REGISTRO DE MANOBRA FECHADO – EXISTENTE
- DESCARGA – PROJETADA
- DESCARGA – EXISTENTE
- BOOSTER – PROJETADO
- BOOSTER – EXISTENTE
- VÁLVULA REDUTORA DE PRESSÃO – PROJETADA
- VÁLVULA REDUTORA DE PRESSÃO – EXISTENTE

NOTAS

01 – DIMENSÕES EM METROS, EXCETO ONDE INDICADO.

02 – CONFIRMAR A POSIÇÃO E A PROFUNDIDADE DAS TUBULAÇÕES EXISTENTES NA OBRA

03 – OS DANOS CAUSADOS AS INSTALAÇÕES SUBTERRÂNEAS SERÃO DE INTEIRA RESPONSABILIDADE DA EXECUTORA DAS OBRAS, INDEPENDENTEMENTE DA INTERFERÊNCIA CONSTAR OU NÃO NOS DESENHOS.

04 – REPOR E COMPACTAR OS LOCAIS ESCAVADOS COM MATERIAL APROPRIADO.

05 – REPOR GRAMAS E CALÇADAS, AS PAVIMENTAÇÕES EXISTENTES DEVERÃO SER RECONSTITUÍDAS.

06 – AS PROTEÇÕES DOS REGISTROS EM PASSEIO DEVERÃO SER EXECUTADOS CONFORME MOS 4ª Ed. MÓDULO 9.

07 – AS QUANTIDADES APRESENTADAS FORAM CALCULADAS COM BASE NA GEOMETRIA DOS TRECHOS DAS TUBULAÇÕES, FUNDAMENTADAS NO ARQUIVO DE CADASTRO DA REDE DE DISTRIBUIÇÃO (CTA). AS MEDIDAS DOS TRECHOS FORAM ARREDONDADAS PARA O PRÓXIMO NÚMERO INTEIRO. NÃO FORAM CONSIDERADAS PERDAS OU QUAISQUER QUANTIDADES ALÉM DAS MEDIDAS.

SANEPAR *Companhia de Saneamento do Paraná*

MUNICÍPIO/SISTEMA:
GENERAL CARNEIRO - JANGADA DO SUL
SISTEMA DE ABASTECIMENTO DE ÁGUA

BLOCO Nº: FOLHA Nº:
02 - 02/03

PROJETO/UNIDADE CONSTRUTIVA:
AMPLIAÇÃO DO SISTEMA DE ABASTECIMENTO DE ÁGUA
REDE DE DISTRIBUIÇÃO DE ÁGUA (RDA)
DETALHAMENTO DE INTERLIGAÇÕES E MELHORIAS

DATA: JULHO/2023

ESCALA: 1:1.000

GERÊNCIA DA SANEPAR
GPOSD
Gerência Projetos e Obras Sudeste
R. Monte Alverne nº564 - Jardim Carvalho – CEP 84016-010 – Ponta Grossa – PR
GERENTE: JOEL PIRES — CREA Nº: 100.276 - D/PR
COORDENADOR GERAL DO PROJETO: DENIS SCHECHTEL NEVES — CREA Nº: 09402617/PR
FISCALIZAÇÃO DO PROJETO CIVIL/SANEAMENTO: DIOGENES VERGES — CREA Nº: 78.132 - D/PR
FISCALIZAÇÃO PROJ. ESTRUT. GEOTEC.: DIOGENES VERGES — CREA Nº: 78.132 - D/PR
FISCALIZAÇÃO DO PROJETO MECÂNICO: ARTHUR VIEIRA NETO — CREA Nº: 107.842 - D/PR
FISCALIZAÇÃO DO PROJ. ELETRICO E AUTOM.: —
FISCALIZAÇÃO DO PROJ. UNIDADES LINEARES: —
DESENVOLVIMENTO DO DESENHO: —
ADEQUAÇÃO DO DESENHO: —

EMPRESA CONTRATADA
SJMH
S.J.M.H. Engenharia e Construções Ltda.
R. Marechal Deodoro nº500, Sala 164 - CEP 80010-010 - Curitiba-PR - e-mail: sjmh@sjmh.com.br
RESP. TÉCNICO DO PROJETO: SONG JON SCREMIN — CREA Nº: 166.833 - D/PR
RESP. TÉCNICO DO PROJETO: -- — CREA Nº: --
ARQUIVO ELETRÔNICO: 002-SAA-0674-9142-PBHI-DE-0000RDA01DETALHAMENTO-R0

A1 NORMAL – SJMH