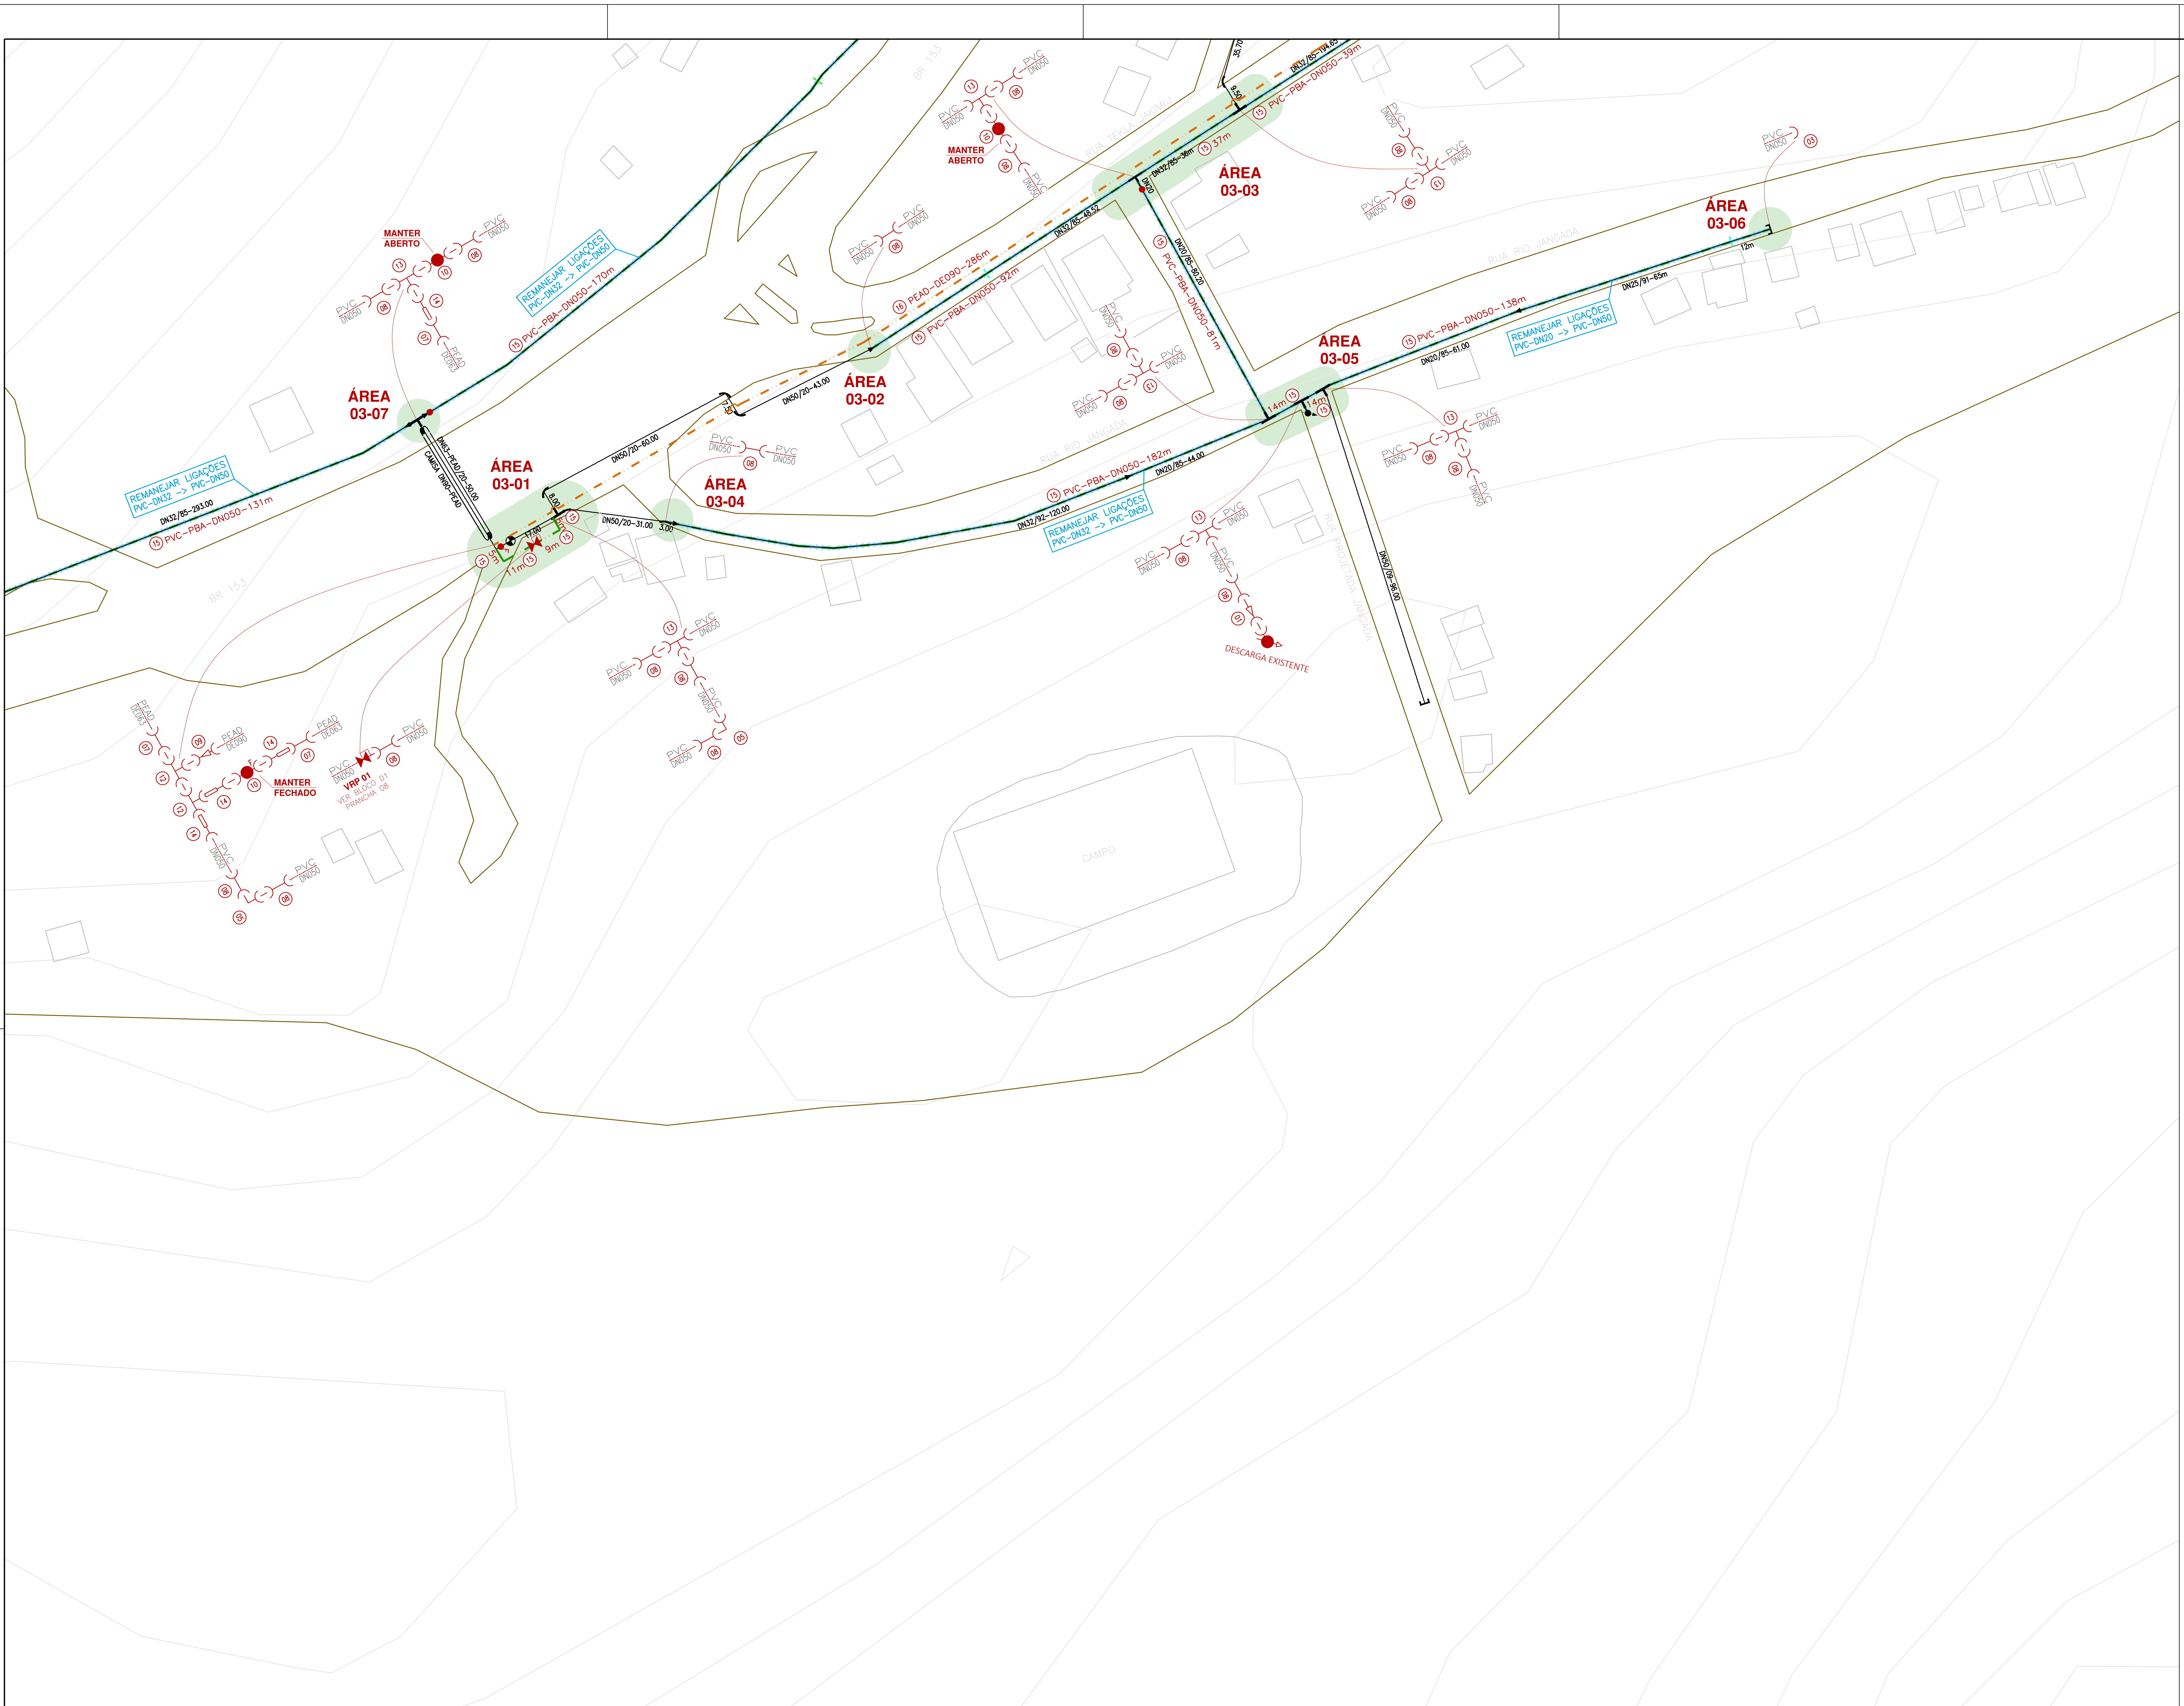

RELAÇÃO DE EQUIPAMENTOS E MATERIAIS

REDE DE DISTRIBUIÇÃO DE ÁGUA

COD.	Nº	DISCRIMINAÇÃO	QT.	UN.
		ÁREA-03-01		
22543	05	CURVA PVC JE PB 90 COM ANEL NBR 5647 DN50	2	PÇ
294924	07	LUVA POLIETILENO PE 100 PN16 PARA ELETROFUSAO DE 63	2	PÇ
23930	08	LUVA DE CORRER PVC JE COM ANEIS NBR 5647 DN50	6	PÇ
309418	09	REDUCAO POLIETILENO PE 100 PN16 PARA ELETROFUSAO DE 90 DE 63	1	PÇ
280186	10	REGISTRO GAVETA FD COM CUNHA ELASTICA JE PARA PVC PBA COM CABECOTE E ANEIS DN50 (MANTER FECHADO)	1	PÇ
309331	12	TE POLIETILENO PARA ELETROFUSAO BBB (OU KIT TE BBP MAIS LUVA) PE 100 PN16 DE 63	2	PÇ
26204	13	TE PVC JE BBB COM ANEIS DN50	1	PÇ
310410	14	LUVA TRANSICAO POLIETILENO PE 100 PN16 ELETROFUSAO ROSCA MACHO DE 63 POL 2"	3	PÇ
30791		LUVA FG BSP POL 2"	3	PÇ
20117		ADAPTADOR PVC JE BOLSA/ROSCA COM ANEL DN50 POL 2"	3	PÇ
		ÁREA-03-02		
23930	08	LUVA DE CORRER PVC JE COM ANEIS NBR 5647 DN50	1	PÇ
		ÁREA-03-03		
23930	08	LUVA DE CORRER PVC JE COM ANEIS NBR 5647 DN50	4	PÇ
280186	10	REGISTRO GAVETA FD COM CUNHA ELASTICA JE PARA PVC PBA COM CABECOTE E ANEIS DN50	1	PÇ
26204	13	TE PVC JE BBB COM ANEIS DN50	2	PÇ
		ÁREA-03-04		
23930	08	LUVA DE CORRER PVC JE COM ANEIS NBR 5647 DN50	1	PÇ
		ÁREA-03-05		
301090	01	BUCHA DE REDUCAO LONGA PVC-U JS PB PN750KPA NBR 5648 DE 50 DE 20	1	PÇ
23930	08	LUVA DE CORRER PVC JE COM ANEIS NBR 5647 DN50	6	PÇ
26204	13	TE PVC JE BBB COM ANEIS DN50	3	PÇ
		ÁREA-03-06		
20630	03	CAP PVC JE COM ANEL DN50	1	PÇ
		ÁREA-03-07		
294924	07	LUVA POLIETILENO PE 100 PN16 PARA ELETROFUSAO DE 63	1	PÇ
23930	08	LUVA DE CORRER PVC JE COM ANEIS NBR 5647 DN50	2	PÇ
280186	10	REGISTRO GAVETA FD COM CUNHA ELASTICA JE PARA PVC PBA COM CABECOTE E ANEIS DN50	1	PÇ
26204	13	TE PVC JE BBB COM ANEIS DN50	1	PÇ
310410	14	LUVA TRANSICAO POLIETILENO PE 100 PN16 ELETROFUSAO ROSCA MACHO DE 63 POL 2"	1	PÇ
30791		LUVA FG BSP POL 2"	1	PÇ
20117		ADAPTADOR PVC JE BOLSA/ROSCA COM ANEL DN50 POL 2"	1	PÇ
		TUBULAÇÕES DA PRANCHA		
27570	15	TUBO PVC JEI PB PN 0,60 MPA – NBR 5647 (COMPRIMENTO TOTAL 6M UTIL 5,88M) DN50	928	m
298741	16	TUBO POLIETILENO PE 100 PN10 (ROLO COM 50,0 M) DE 90	286	m
		PROTEÇÃO PARA REGISTRO EM PASSEIO		
275174	S/N	TAMPA PLASTICA PARA REGISTRO PASSEIO – TPP PADRAO SANEPAR	3	PÇ
		DESCARGA EXISTENTE (TROCAR O REGISTRO)		
280186	10	REGISTRO GAVETA FD COM CUNHA ELASTICA JE PARA PVC PBA COM CABECOTE E ANEIS DN50	3	PÇ

ARTICULAÇÃO DAS PRANCHAS

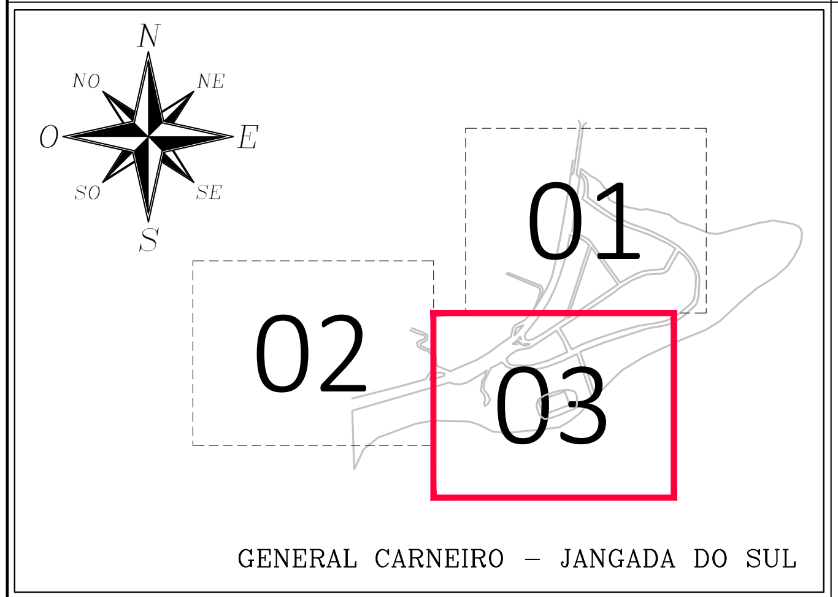

CONVENÇÕES – REDE DE DISTRIBUIÇÃO

- PVC PBA DN50
- PEAD DE90
- LIMITES DAS ZONAS DE PRESSÃO
- LIMITES DOS SETORES DE MANOBRA
- TUBULAÇÕES EXISTENTES
- TUBULAÇÕES VIRGENS
- REDE À DESATIVAR
- REDE À SUBSTITUIR
- HIDROGRAFIA

LEGENDA

- CAP
- CURVA 22 PB
- CURVA 45 PB
- CURVA 90 PB
- CURVA 11 BB
- CURVA 22 BB
- CURVA 45 BB
- CURVA 90 BB
- LUVA BB
- REDUÇÃO BB
- REDUÇÃO PB
- EXTREMIDADE FB
- EXTREMIDADE FP
- TRANSIÇÃO
- COLARINHO E FLANGE
- CRUZETA BBBB
- TÊ BBB
- TÊ DE REDUÇÃO BBB
- JUNÇÃO BBB
- HIDRANTE
- MACROMEDIDOR
- VENTOSA
- ● REGISTRO DE MANOBRA ABERTO – PROJETADO
- ● REGISTRO DE MANOBRA ABERTO – EXISTENTE
- ● REGISTRO DE MANOBRA FECHADO – PROJETADO
- ● REGISTRO DE MANOBRA FECHADO – EXISTENTE
- DESCARGA – PROJETADA
- DESCARGA – EXISTENTE
- ▨ BOOSTER – PROJETADO
- ▨ BOOSTER – EXISTENTE
- VÁLVULA REDUTORA DE PRESSÃO – PROJETADA
- VÁLVULA REDUTORA DE PRESSÃO – EXISTENTE

NOTAS

01 – DIMENSÕES EM METROS, EXCETO ONDE INDICADO.

02 – CONFIRMAR A POSIÇÃO E A PROFUNDIDADE DAS TUBULAÇÕES EXISTENTES NA OBRA

03 – OS DANOS CAUSADOS ÀS INSTALAÇÕES SUBTERRÂNEAS SERÃO DE INTEIRA RESPONSABILIDADE DA EXECUTORA DAS OBRAS, INDEPENDENTEMENTE DA INTERFERÊNCIA CONSTAR OU NÃO NOS DESENHOS.

04 – REPOR E COMPACTAR OS LOCAIS ESCAVADOS COM MATERIAL APROPRIADO.

05 – REPOR GRAMAS E CALÇADAS, AS PAVIMENTAÇÕES EXISTENTES DEVERÃO SER RECONSTITUÍDAS.

06 – AS PROTEÇÕES DOS REGISTROS EM PASSEIO DEVERÃO SER EXECUTADOS CONFORME MOS 4º Ed. MÓDULO 9.

07 – AS QUANTIDADES APRESENTADAS FORAM CALCULADAS COM BASE NA GEOMETRIA DOS TRECHOS DAS TUBULAÇÕES, FUNDAMENTADAS NO ARQUIVO DE CADASTRO DA REDE DE DISTRIBUIÇÃO (CTA). AS MEDIDAS DOS TRECHOS FORAM ARREDONDADAS PARA O PRÓXIMO NÚMERO INTEIRO. NÃO FORAM CONSIDERADAS PERDAS OU QUAISQUER QUANTIDADES ALÉM DAS MEDIDAS.

SANEPAR *Companhia de Saneamento do Paraná*

MUNICÍPIO/SISTEMA:
GENERAL CARNEIRO - JANGADA DO SUL
SISTEMA DE ABASTECIMENTO DE ÁGUA

BLOCO Nº: 02 - FOLHA Nº: 03/03

PROJETO/UNIDADE CONSTRUTIVA:
AMPLIAÇÃO DO SISTEMA DE ABASTECIMENTO DE ÁGUA
REDE DE DISTRIBUIÇÃO DE ÁGUA (RDA)
DETALHAMENTO DE INTERLIGAÇÕES E MELHORIAS

DATA: JULHO/2023

ESCALA: 1:1.000

GERÊNCIA DA SANEPAR
GPOSD
Gerência Projetos e Obras Sudeste
R. Monte Alverne nº644 – Jardim Carvalho – CEP 84016-010 – Ponta Grossa – PR
GERENTE: JOEL PIRES CREA Nº: 100.276 - D/PR

COORDENADOR GERAL DO PROJETO: DENIS SCHECHTEL NEVES CRQ 09402617/PR	FISCALIZAÇÃO DO PROJ. ELÉTRICO E AUTOM.: - -
FISCALIZAÇÃO DO PROJETO CIVIL/HIDRÁULICO: DIÓGENES VERGÈS 78.132 - D/PR	FISCALIZAÇÃO DO PROJ. UNIDADES LINEARES: - -
FISCALIZAÇÃO PROJ. ESTRUT, GEOTÉC. SOND.: DIÓGENES VERGÈS 78.132 - D/PR	DESENVOLVIMENTO DO DESENHO - -
FISCALIZAÇÃO DO PROJETO MECÂNICO: ARTHUR VIEIRA NETO 107.842 - D/PR	ADEQUAÇÃO DO DESENHO - -

EMPRESA CONTRATADA
SJMH
S.J.M.H. Engenharia e Construções Ltda.
R. Marechal Deodoro nº500, Sala 164 - CEP 80010-010 - Curitiba-PR - e-mail: sjmh@sjmh.com.br

RESP. TÉCNICO DO PROJETO: SONG JON SCREMIN CREA Nº: 166.833 - D/PR	RESP. TÉCNICO DO PROJETO: -- CREA Nº: --

ARQUIVO ELETRÔNICO:
003-SAA-0674-9142-PBHI-DE-0000RDA01DETALHAMENTO-R0

A1 NORMAL – SJMH