

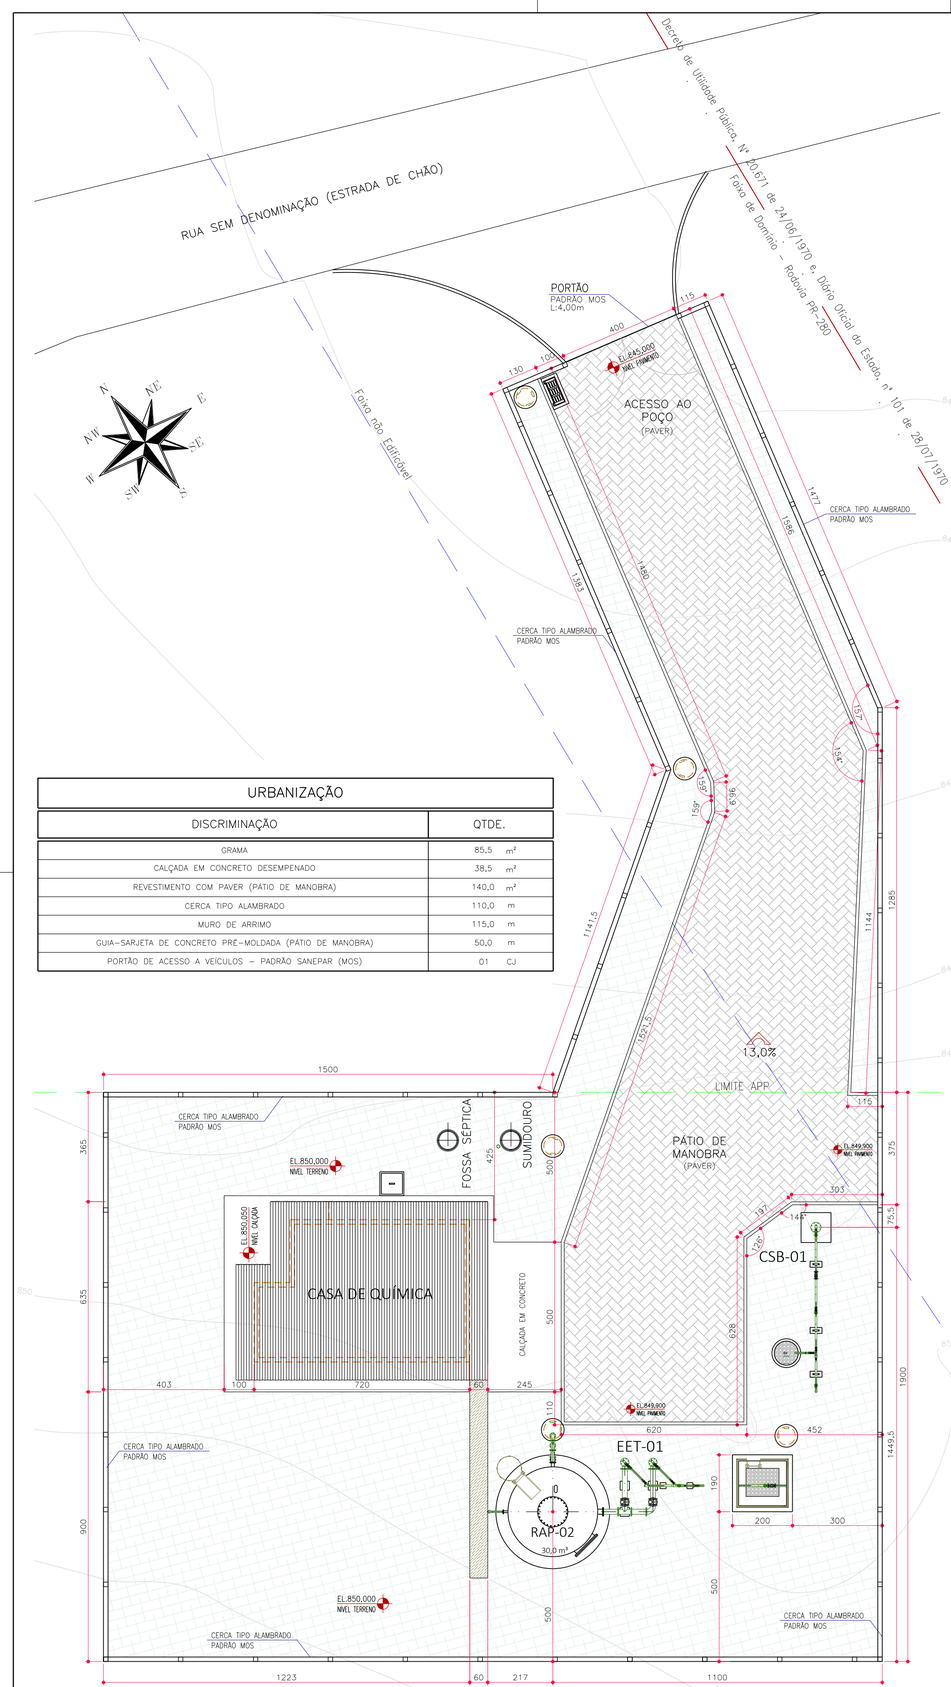


URBANIZAÇÃO		
DISCRIMINAÇÃO	QTDE.	
GRAMA	85,5	m²
CALÇADA EM CONCRETO DESEMPENADO	38,5	m²
REVESTIMENTO COM PAVER (PÁTIO DE MANOBRA)	140,0	m²
CERCA TIPO ALAMBRADO	110,0	m
MURO DE ARRIMO	115,0	m
GUIA-SARJETA DE CONCRETO PRÉ-MOLDADA (PÁTIO DE MANOBRA)	50,0	m
PORTÃO DE ACESSO A VEÍCULOS - PADRÃO SANEPAR (MOS)	01	CJ


NOVO PÁTIO DE RESERVAÇÃO E CAPTAÇÃO
LAYOUT DE AMARRAÇÃO
ESCALA 1:100

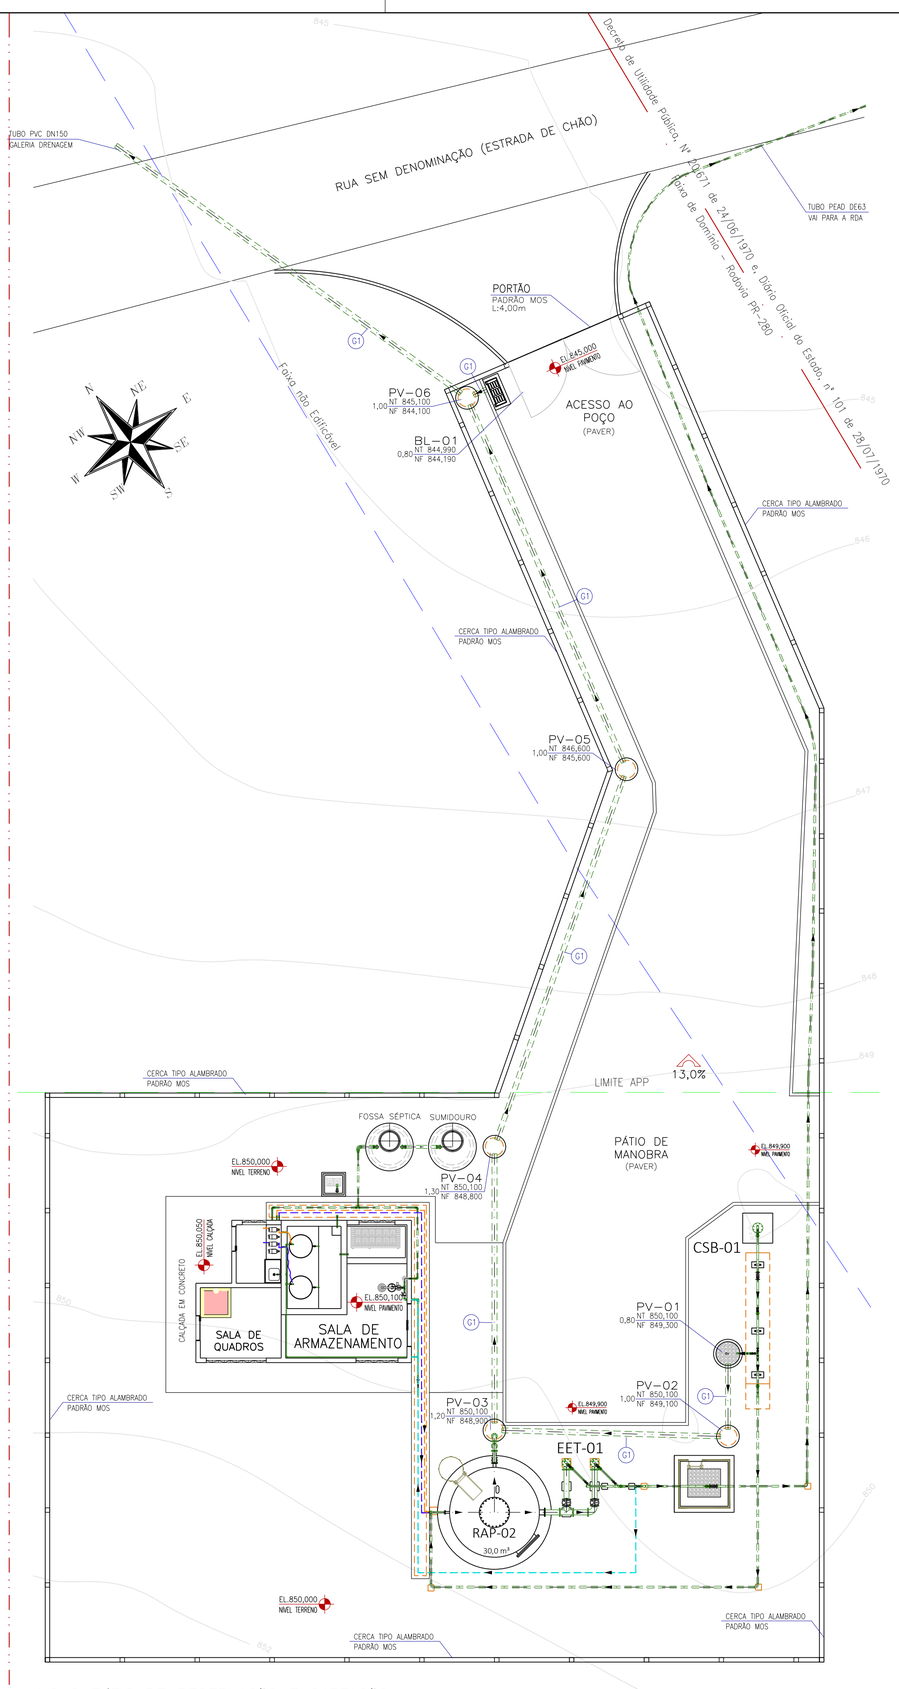

NOVO PÁTIO DE RESERVAÇÃO E CAPTAÇÃO
LAYOUT DA GALERIA DE DRENAGEM
ESCALA 1:100

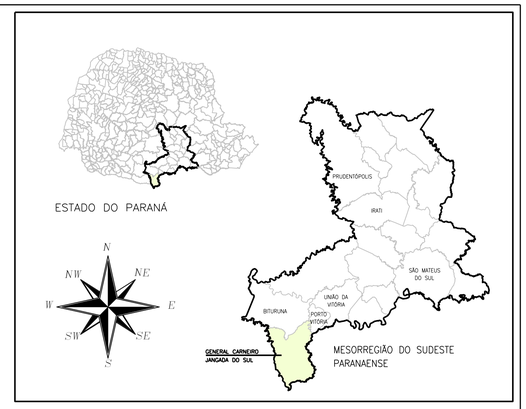

CAPTAÇÃO SUBTERRÂNEA – CSB-02
CROQUI DE LOCALIZAÇÃO
SEM ESCALA

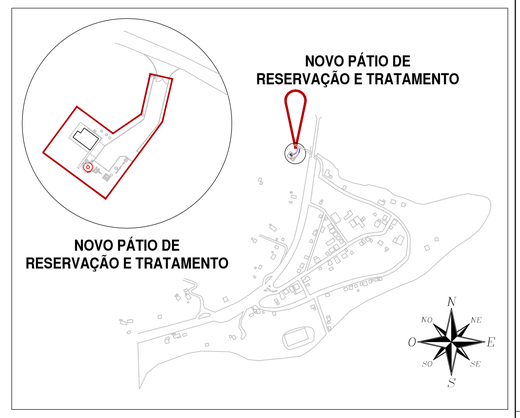

MUNICÍPIO DE GENERAL CARNEIRO – JANGADA DO SUL
CROQUI DE LOCALIZAÇÃO
SEM ESCALA

COORDENADAS:
X=474334,540 m
Y=7083047,830 m

RELAÇÃO DE EQUIP. E MATERIAIS				
NOVO PÁTIO DE RESERVAÇÃO E CAPTAÇÃO				
COD.	Nº	DISCRIMINAÇÃO	QT.	UN.
DRENAGEM				
304347	G1	TUBO PVC-O DEFOFO JEI PB PN 12,5 MRS 45 FAIXA OCRE PARA PARA ESGOTO (6M) (COMPRIMENTO UTIL 5,75M) DN150	70,0	m
304469	S/N	CONJUNTO COMPLETO DE BOCA DE LOBO EM CONCRETO PRÉ-MOLDADO TIPO SIMPLES FCK 20 MPA FORMADO POR GRELHA, CANTONEIRA E CAIXILHO DIMENSIONAL 110 X 52 CM (SOBRECARGA CJ COMPLETO)	01	PÇ

NOTAS

01 – DIMENSÕES EM CENTIMETROS E ELEVAÇÕES EM METROS, EXCETO ONDE INDICADO.

02 – CONFIRMAR A POSIÇÃO E A PROFUNDIDADE DAS TUBULAÇÕES EXISTENTES NA OBRA.

03 – OS DANOS CAUSADOS ÀS INSTALAÇÕES SUBTERRÂNEAS SERÃO DE INTEIRA RESPONSABILIDADE DA EXECUTORA DAS OBRAS, INDEPENDENTEMENTE DA INTERFERÊNCIA CONSTAR OU NÃO NOS DESENHOS.

04 – O PROJETO BÁSICO HIDRÁULICO FOI COMPATIBILIZADO COM OS DEMAIS PROJETOS CONTRATADOS, CONFORME AS ESPECIALIDADES LISTADAS ABAIXO.

PROJETO/SERVIÇO	DESENVOLVIMENTO
BÁSICO HIDRÁULICO	S.J.M.H. ENGENHARIA E CONSTRUÇÕES LTDA.
TOPOGRAFIA	SOCIEDADE DA ÁGUA SERVIÇOES AMBIENTAIS E GEOTECNOLOGIAS
BÁSICO ELÉTRICO/AUTOMAÇÃO	S.J.M.H. ENGENHARIA E CONSTRUÇÕES LTDA.
BÁSICO MECÂNICO/ESPECIFICAÇÕES	S.J.M.H. ENGENHARIA E CONSTRUÇÕES LTDA.
SONDAGENS SPT	GEOLOC LOCAÇÕES E SONDAGENS LTDA.
BÁSICO ESTRUTURAL	S.J.M.H. ENGENHARIA E CONSTRUÇÕES LTDA.
BÁSICO GEOTÉCNICO	S.J.M.H. ENGENHARIA E CONSTRUÇÕES LTDA.

SANEPAR Companhia de Saneamento do Paraná

MUNICÍPIO/SISTEMA:
GENERAL CARNEIRO - JANGADA DO SUL
SISTEMA DE ABASTECIMENTO DE ÁGUA

BLOCO Nº: FOLHA Nº:
01 - 01/09

PROJETO/UNIDADE CONSTRUTIVA:
PROJETO BÁSICO HIDRÁULICO
CAPTAÇÃO SUBTERRÂNEA - CSB-01 / EEB-01
LAYOUT DE AMARRAÇÃO E DRENAGEM

DATA: AGOSTO/2023

ESCALA: INDICADA

GERÊNCIA DA SANEPAR
GPOSD
Gerência Projetos e Obras Sudeste
R. Monte Alverne nº644 - Jardim Carvalho - CEP 84016-010 - Ponta Grossa - PR

GERENTE: JOEL PIRES CREA Nº: 100.276 - D/PR

COORDENADOR GERAL DO PROJETO: DENIS SCHECHTEL NEVES CREA 094026177/PR	FISCALIZAÇÃO DO PROJ. ELETRICO E AUTOM.: -
FISCALIZAÇÃO DO PROJETO CIVIL/HIDRÁULICO: DIOGENES VERGÉS 78.132 - D/PR	FISCALIZAÇÃO DO PROJ. UNIDADES LINEARES: -
FISCALIZAÇÃO DO PROJ. ESTRUT. CONCRETO: DIOGENES VERGÉS 78.132 - D/PR	DESENVOLVIMENTO DO DESENHO: -
FISCALIZAÇÃO DO PROJETO MECÂNICO: ARTHUR VIEIRA NETO 107.842 - D/PR	ADEQUAÇÃO DO DESENHO: -

EMPRESA CONTRATADA
SJMH
S.J.M.H. Engenharia e Construções Ltda.
R. Marechal Deodoro nº530, Sala 164 - CEP 80010-010 - Curitiba-PR - e-mail: sjmh@sjmh.com.br

RESP. TÉCNICO DO PROJETO: SONG JON SCREMIN CREA Nº: 166.833 - D/PR	RESP. TÉCNICO DO PROJETO: -- CREA Nº: --

ARQUIVO ELETRÔNICO:
001-SAA-0674-9142-PBHI-DE-0000GER000PATIOAMARDRE-R0

A1 NORMAL – SJMH