

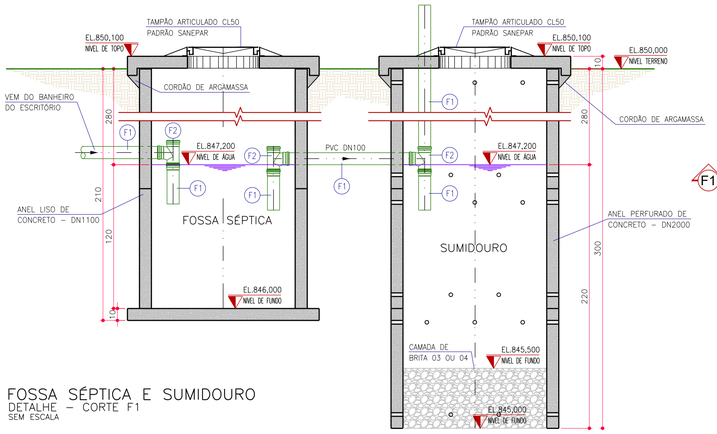



FOSSA SÉPTICA E SUMIDOURO
DETALHE – CORTE F1
SEM ESCALA

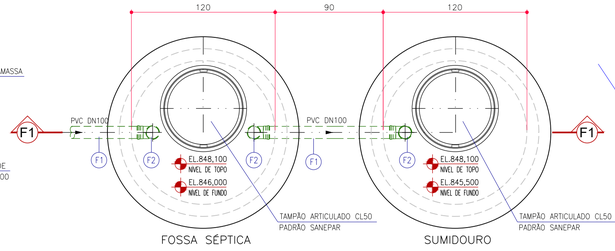

FOSSA SÉPTICA E SUMIDOURO
DETALHE – PLANTA
SEM ESCALA

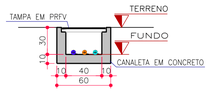

CANALETA DE TUBULAÇÕES
DETALHAMENTO
SEM ESCALA

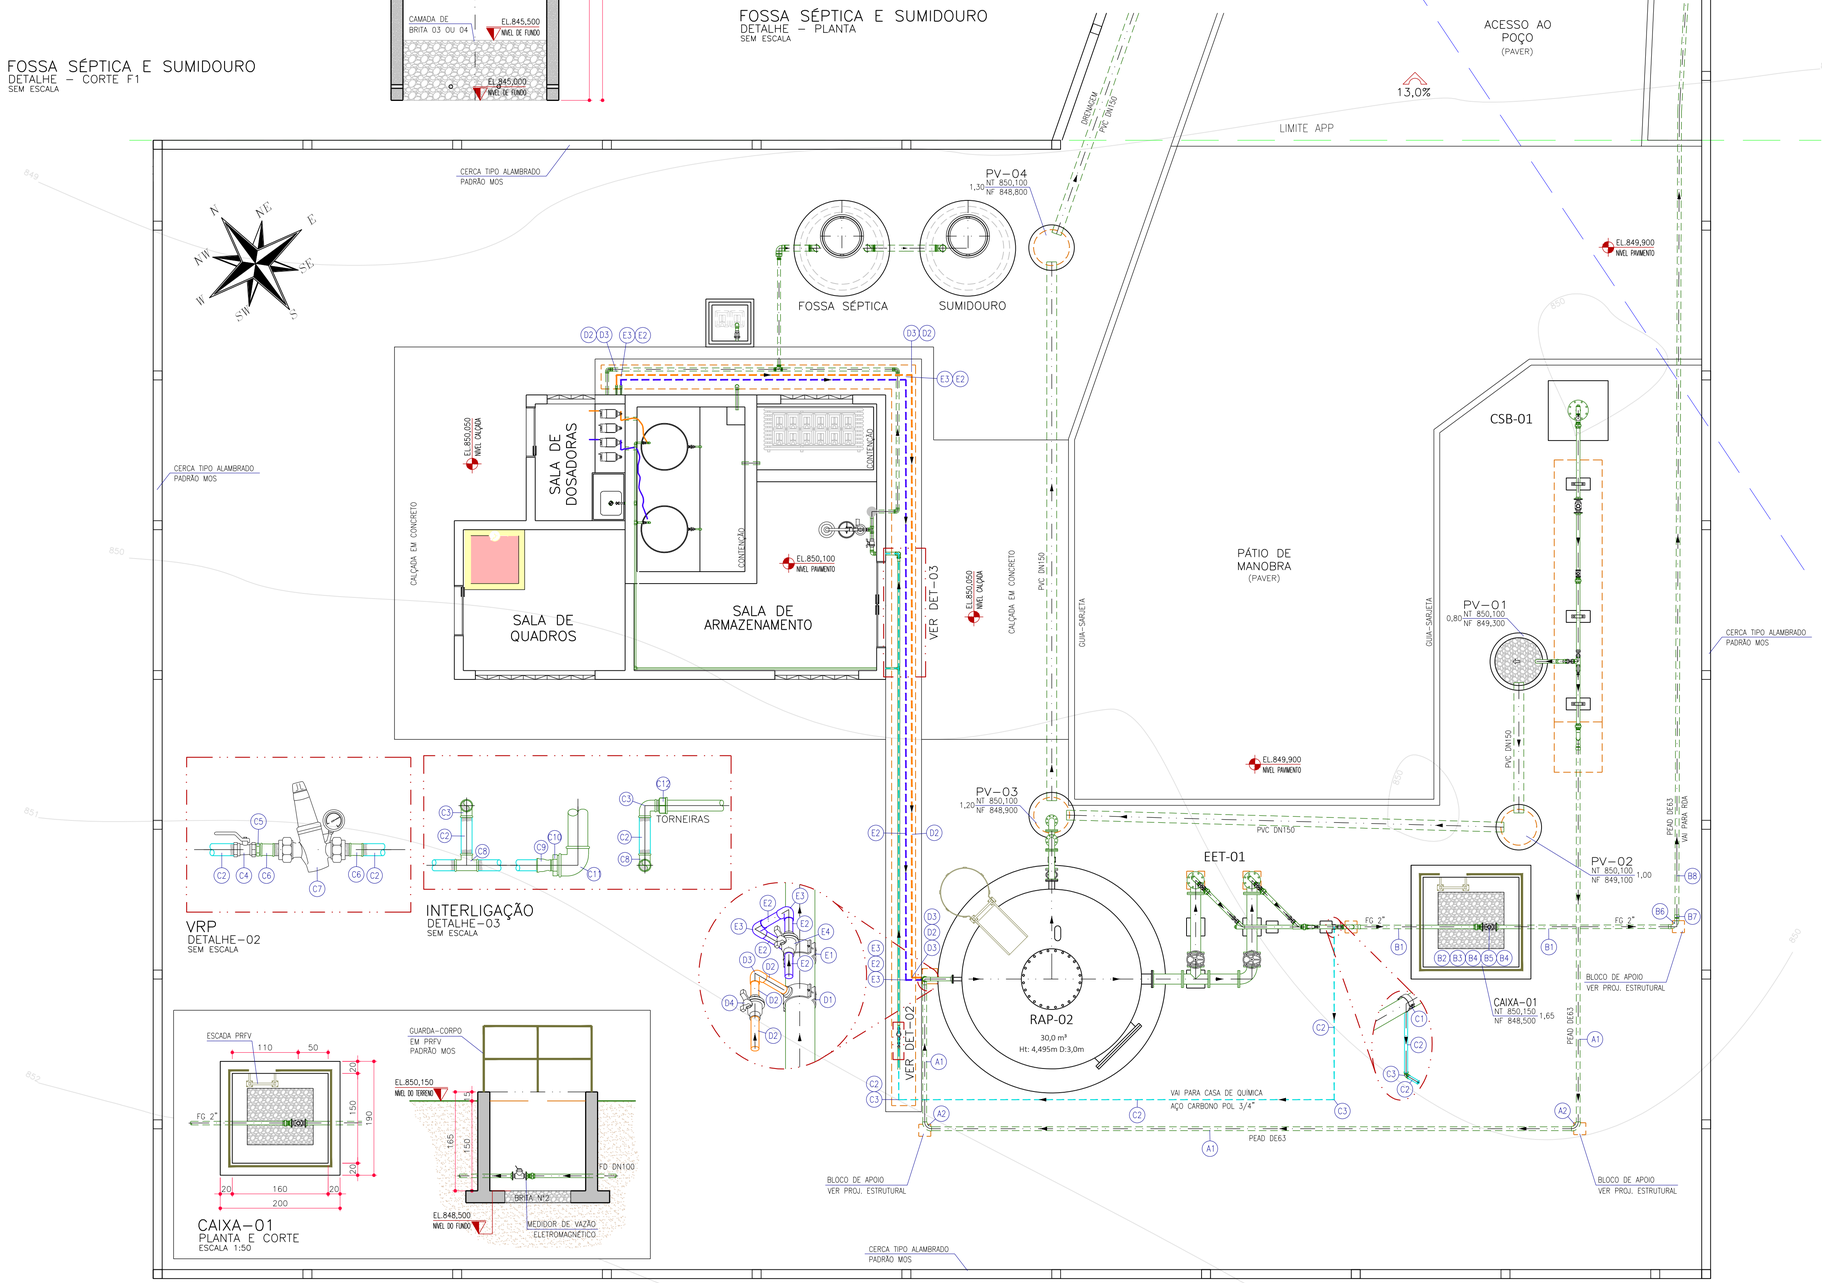

VRP
DETALHE-02
SEM ESCALA

INTERLIGAÇÃO
DETALHE-03
SEM ESCALA

CAIXA-01
PLANTA E CORTE
ESCALA 1:50

NOVO PÁTIO DE RESERVAÇÃO E CAPTAÇÃO
LAYOUT DE INTERLIGAÇÃO
ESCALA 1:50

RELAÇÃO DE EQUIP. E MATERIAIS

NOVO PÁTIO DE RESERVAÇÃO E CAPTAÇÃO

COD.	Nº	DISCRIMINAÇÃO	QT.	UN.
		CBS-01 PARA RAP-02		
298738	A1	TUBO POLIETILENO PE 100 PN10 (ROLO COM 50,0 M) DE 63	20,5	m
309982	A2	CURVA POLIETILENO INJETADA 90 TERMOFUSAO PE 100 PN10 DE 63	02	PÇ
		SAÍDA D'ÁGUA TRATADA PARA A RDA		
306724	B1	TUBO ACO CARBONO GALVANIZADO A FOGO CLASSE PRESSAO MEDIA COM COSTURA LONGITUDINAL 6M (S/REBARBA INTERNA OXIDO ZINCO OLEO TAMPAS) ROSCA BSP POL 2"	5,0	m
134880	B2	UNIAO FG ASSENTO CONICO BRONZE BSP POL 2"	01	PÇ
30937	B3	NIPLE FG BSP POL 2"	01	PÇ
30538	B4	FLANGE FG COM SEXTAVADO BSP POL 2"	02	PÇ
** 291669	B5	HIDROMETRO ULTRASSONICO QN 25,0 M3/HORA CLASSE C DN50 POL 2"	01	PÇ
134163	B6	CURVA FG FEMEA/FEMEA 90° BSP POL 2"	01	PÇ
303132	B7	ADAPTADOR DE TRANSICAO PEAD/PP/PLAST.ENG. BB JUNTA DE COMPRESSAO/ROSCA BSP FEMEA ACESSORIOS ACO INOX 304 PVC NBR 5647 PEAD NBR 15561 PN16 DE 63 POL 2"	01	PÇ
298738	B8	TUBO POLIETILENO PE 100 PN10 (ROLO COM 50,0 M) DE 63	50,0	m
		ÁGUA PARA A ALIMENTAÇÃO DA CASA DE QUÍMICA		
** 655	C1	COLAR TOMADA FD DN100 POL 3/4"	01	PÇ
311123	C2	TUBO DE ACO CARBONO GALVANIZADO A FOGO CLASSE PRESSAO PESADA COM COSTURA LONGITUDINAL 6M ROSCA BSP POL 3/4"	24,0	m
29696	C3	COTOVELO FG BSP POL 3/4"	04	PÇ
302109	C4	VALVULA ESFERA TRIPARTIDA CORPO ESFERA ALAVANCA EM INOX 304/CF8 PASSAGEM PLENA VEDACAO PTFE PN 20 (CLASSE 300) ROSCA BSP POL 3/4"	01	PÇ
30899	C5	NIPLE FG BSP POL 3/4"	01	PÇ
30759	C6	LUVA FG BSP POL 3/4"	02	PÇ
30082	C7	VALVULA REDUTORA DE PRESSAO ACAO DIRETA PRESSAO DE ENTRADA ATE 10 BAR SAIDA AJUSTAVEL 1,0 A 3,0 BAR ROSCA BSP POL 3/4"	01	PÇ
31437	C8	TE FG BSP POL 3/4"	01	PÇ
31135	C9	LUVA REDUCAO FG BSP POL 1" POL 3/4"	01	PÇ
116025	C10	NIPLE REDUCAO FG BSP POL 1.1/2" POL 1"	01	PÇ
29726	C11	COTOVELO FG BSP POL 1.1/2"	01	PÇ
20079	C12	ADAPTADOR CURTO PVC-U JS BOLSA/ROSCA MACHO PN750KPA NBR 5648 DE 25 POL 3/4	01	PÇ
		ÁCIDO FLUOSSILÍCICO		
** 310776	D1	COLAR TOMADA FD DN80 POL 3/4"	01	PÇ
300889	D2	TUBO PVC SCH80 JS PN10 DE25MM ASTM D1785 NSF/ANSI STD 14&61 FDA 21	17,0	m
301259	D3	JOELHO PVC JS 90 SCH80 PN10 DE25MM ASTM D2467 NSF/ANSI STD 14&61 FDA 21	05	PÇ
312436	D4	VALVULA ESFERA PVC JS UMA UNIAO VOLANTE 1/4 VOLTA VEDACAO CORPO BORRACHA NITRILICA ESFERA PTFE OU PP PN750KPA NBR 5648 DE 25	01	PÇ
		HIPOCLORITO DE SÓDIO		
** 310776	E1	COLAR TOMADA FD DN80 POL 3/4"	01	PÇ
300385	E2	TUBO CPVC SCH80 SOLDAVEL PN10 P/ TUBULACAO DE25MM ASTM F441 NSF/ANSI STD 14&61 FDA 21 DE 25	17,0	m
300490	E3	CURVA CPVC JS BB 90 PN10 SCHEDULE 80 ASTM F439 NSF/ANSI STD 14&61 FDA 21 DE 25	06	PÇ
300590	E4	VALVULA ESFERA DUPLA UNIAO CPVC JS BB SCH80 ACIONAMENTO MANUAL POR VOLANTE EN ISO 16135 (ASTM F441/F439) NSF/ANSI STD14/61 FDA 21 POL 3/4"	01	PÇ
		FOSSA SÉPTICA E SUMIDOURO		
312103	F1	TUBO PVC-U JS PB (DUPLA ATUACAO) PARA ESGOTO PREDIAL E AGUA PLUVIAL NBR 5688 SERIE NORMAL 3M DN 100	03	PÇ
312351	F2	TE PVC-U JEI BBP PARA ESGOTO PREDIAL E AGUA PLUVIAL NBR 5688 SERIE NORMAL DN100	03	PÇ
270350	S/N	TAMPAO FD CLASSE 50 PARA POCO DE VISITA PADRAO SANEPAR	02	PÇ
		ACESSÓRIOS PARA CONEXÕES FLANGEADAS		
326621	S/N	KIT PARAFUSO PORCA ARRUELA LISA ACO CARBONO ARRUELA VEDACAO FURACAO PN 10 NBR 7675 DN 50	02	PÇ
		PEÇAS EM PRFV – ACESSO E SEGURANÇA		
** 313629	S/N	ESCADA TIPO MARINHEIRO PRFV SEM GAIOLA ALTURA MENOR QUE 3,5M	01 1,50	CJ m
** 327176	S/N	GUARDA CORPO PRFV INSTALADO NA SUPERFICIE (COM SAPATA)	6,15	m
** 311747	S/N	GRADE DE PISO PRFV VAO 0,4 X 1,0M GR 0,6X1,2M	18	UN

• VER ESPECIFICAÇÃO TÉCNICA.
•• VER ESPECIFICAÇÃO BÁSICA CÓDIGOS SAM.

NOTAS

01 – DIMENSÕES EM CENTÍMETROS E ELEVAÇÕES EM METROS, EXCETO ONDE INDICADO.

02 – CONFIRMAR A POSIÇÃO E A PROFUNDIDADE DAS TUBULAÇÕES EXISTENTES NA OBRA.

03 – OS DANOS CAUSADOS ÀS INSTALAÇÕES SUBTERRÂNEAS SERÃO DE INTEIRA RESPONSABILIDADE DA EXECUTORA DAS OBRAS, INDEPENDENTEMENTE DA INTERFERÊNCIA CONSTAR OU NÃO NOS DESENHOS.

04 – O PROJETO BÁSICO HIDRÁULICO FOI COMPATIBILIZADO COM OS DEMAIS PROJETOS CONTRATADOS, CONFORME AS ESPECIALIDADES LISTADAS ABAIXO.

PROJETO/SERVIÇO	DESENVOLVIMENTO
BÁSICO HIDRÁULICO	S.J.M.H. ENGENHARIA E CONSTRUÇÕES LTDA.
TOPOGRAFIA	SOCIEDADE DA ÁGUA SERVIÇOES AMBIENTAIS E GEOTECNOLOGIAS
BÁSICO ELÉTRICO/AUTOMAÇÃO	S.J.M.H. ENGENHARIA E CONSTRUÇÕES LTDA.
BÁSICO MECÂNICO/ESPECIFICAÇÕES	S.J.M.H. ENGENHARIA E CONSTRUÇÕES LTDA.
SONDAGENS SPT	GEOLOC LOCAÇÕES E SONDAGENS LTDA.
BÁSICO ESTRUTURAL	S.J.M.H. ENGENHARIA E CONSTRUÇÕES LTDA.
BÁSICO GEOTÉCNICO	S.J.M.H. ENGENHARIA E CONSTRUÇÕES LTDA.

SANEPAR *Companhia de Saneamento do Paraná*

MUNICÍPIO/SISTEMA:
GENERAL CARNEIRO - JANGADA DO SUL
SISTEMA DE ABASTECIMENTO DE ÁGUA

BLOCO Nº: FOLHA Nº:
01 - 02/09

PROJETO/UNIDADE CONSTRUTIVA:
PROJETO BÁSICO HIDRÁULICO
CAPTAÇÃO SUBTERRÂNEA - CSB-01 / EEB-01
LAYOUT DE INTERLIGAÇÕES

DATA: AGOSTO/2023

ESCALA: INDICADA

GERÊNCIA DA SANEPAR
GPOSD
Gerência Projetos e Obras Sudeste
R. Monte Alverne nº644 - Jardim Carvalho - CEP 84016-010 - Ponta Grossa – PR
GERENTE: JOEL PIRES CREA Nº: 100.276 - D/PR

COORDENADOR GERAL DO PROJETO: DENIS SCHECHTEL NEVES CREA 094026171/PR	FISCALIZAÇÃO DO PROJ. ELETRICO E AUTOM.: -
FISCALIZAÇÃO DO PROJETO CIVIL/HIDRÁULICO: DIOGENES VERGÉS 78.132 - D/PR	FISCALIZAÇÃO DO PROJ. UNIDADES LINEARES: -
FISCALIZAÇÃO PROJ. ESTRUT., GEOTEC. SOND.: DIOGENES VERGÉS 78.132 - D/PR	DESENVOLVIMENTO DO DESENHO: -
FISCALIZAÇÃO DO PROJETO MECÂNICO: ARTHUR VIEIRA NETO 107.842 - D/PR	ADEQUAÇÃO DO DESENHO: - -

EMPRESA CONTRATADA
S.J.M.H.
S.J.M.H. Engenharia e Construções Ltda.
R. Marechal Deodoro nº580, Sala 164 - CEP 80010-010 - Curitiba/PR - e-mail: sjmh@sjmh.com.br

RESP. TÉCNICO DO PROJETO: SONG JON SCREMIN CREA Nº: 166.833 - D/PR	RESP. TÉCNICO DO PROJETO: -- CREA Nº: --
ARQUIVO ELETRÔNICO: 002-SAA-0674-9142-PBHI-DE-0000GER000PATIOINTERLI-R0	

A1 NORMAL – SJMH