




VENTOSA
DETALHE–01
SEM ESCALA

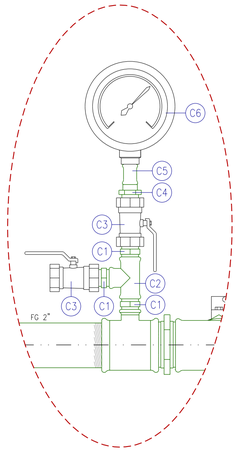

MANÔMETRO E ESFERA
DETALHE–02
SEM ESCALA

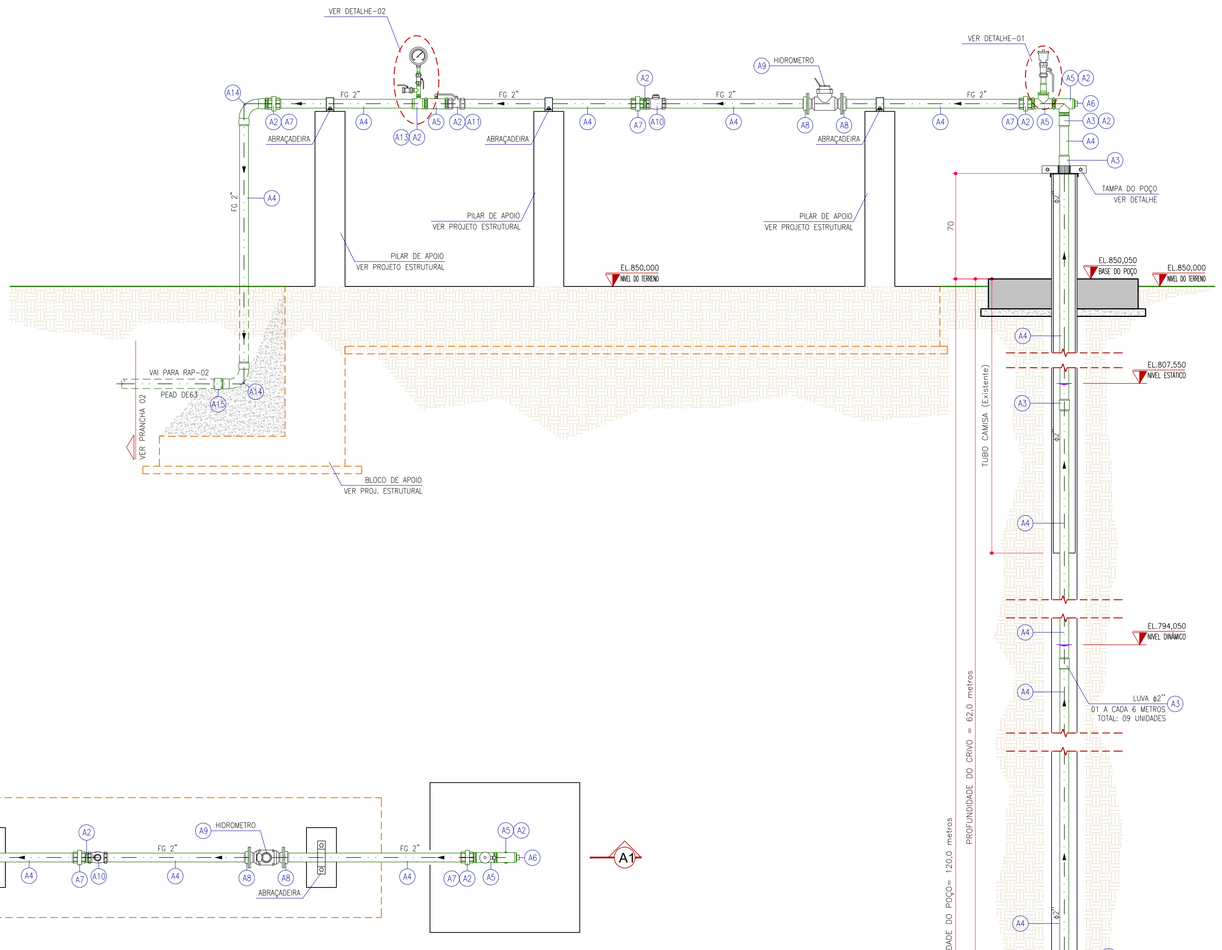


CSB–01 / EEB–01
PLANTA
ESCALA 1:20

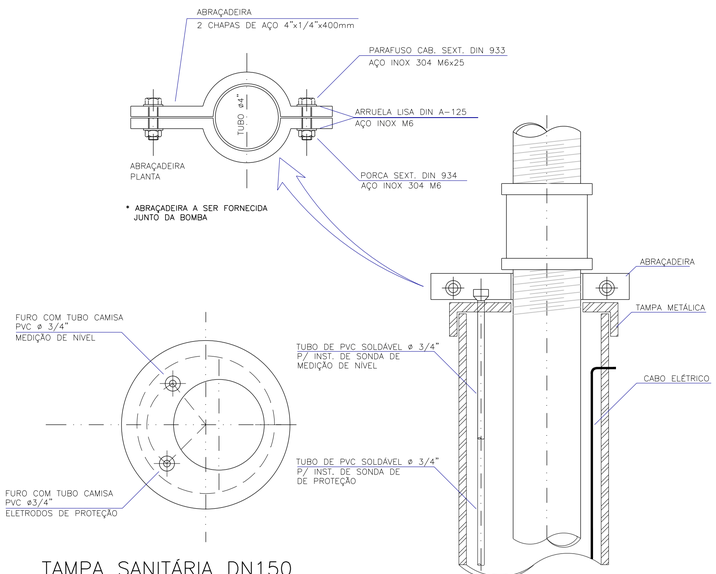

TAMPA SANITÁRIA DN150
DETALHE
SEM ESCALA

DADOS DO POÇO			
NOME	CSB–01 (SIA 5079) – AQUÍFERO GUARANI		
PERFURAÇÃO	02/05/2012	TESTE	17/05/2012
DIÂMETRO CÂMARA	6" de 0,0 a 150,0		
NÍVEL DA BASE	0 m	COTA	850,050 m
NÍVEL ESTÁTICO	42,50 m	COTA	807,550 m
NÍVEL DINÂMICO	56,00 m	COTA	794,050 m
NÍVEL DO CRIVO	62,00 m	COTA	788,050 m
PROFUNDIDADE	120,00 m	COTA	730,050 m
VAZÃO EXPLORÁVEL	10,0 m³/h (2,78 L/s) em 20 h/d		

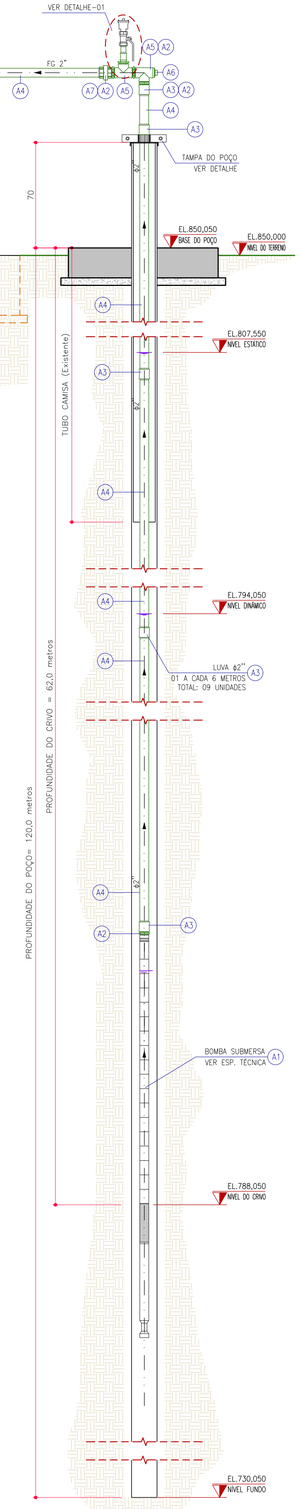

CSB–01 / EEB–01
CORTE A1
ESCALA 1:20

RELAÇÃO DE EQUIPAMENTOS E MATERIAIS

COD.	Nº	DISCRIMINAÇÃO	QT.	UN.
CSB–01 / EEB–01				
* –	A1	MOTOBOMBA SUBMERSA Q: 7,0 m3/h Hm: 63,0 mca	01+01P	CJ
	–	ABRAÇADEIRA PARA POÇO TUBULAÇÃO DE 2" POL (FORNECIMENTO JUNTO COM A BOMBA)	01	CJ
30937	A2	NIPLE FG BSP POL 2"	10	PÇ
30791	A3	LUVA FG BSP POL 2"	11	PÇ
306724	A4	TUBO ACO CARBONO GALVANIZADO A FOGO CLASSE PRESSAO MEDIA COM COSTURA LONGITUDINAL 6M (S/REBARBA INTERNA OXIDO ZINCO OLEO TAMPAS) ROSCA BSP POL 2"	70,0	m
31470	A5	TE FG BSP POL 2"	03	PÇ
31046	A6	BUJAO (PLUG) FG POL BSP POL 2"	01	PÇ
134880	A7	UNIAO FG ASSENTO CONICO BRONZE BSP POL 2"	03	PÇ
30538	A8	FLANGE FG COM SEXTAVADO BSP POL 2"	02	PÇ
** 291669	A9	HIDROMETRO ULTRASSONICO QN 25,0 M3/HORA CLASSE C DN50 POL 2"	01	PÇ
140600	A10	VALVULA RETENCAO BRONZE VERTICAL PN16 BSP POL 2"	01	PÇ
302113	A11	VALVULA ESFERA TRIPARTIDA CORPO ESFERA ALAVANCA EM INOX 304/CF8PASSAGEM PLENA VEDACAO PTFE PN 20 (CLASSE 300) ROSCA BSP POL 2"	02	PÇ
166014	A12	CURVA FG FEMEA/FEMEA 45° BSP POL 2"	01	PÇ
31666	A13	TE REDUCAO FG BSP POL 2" POL 1/2"	01	PÇ
134163	A14	CURVA FG FEMEA/FEMEA 90° BSP POL 2"	02	PÇ
303132	A15	ADAPTADOR DE TRANSICAO PEAD/PP/PLAST.ENG. BB JUNTA DE COMPRESSAO/ROSCA BSP FEMEA ACESSORIOS ACO INOX 304 PVC NBR 5647 PEAD NBR 15561 PN16 DE 63 POL 2"	01	PÇ
** 299956	S/N	TAMPA SANITARIA PARA POCO TUBULAR PROFUNDO 6 X 2 POL	01	PÇ
VENTOSA				
139157	B1	NIPLE REDUCAO FG BSP POL 2" POL 1"	01	PÇ
31429	B2	LUVA FG BSP POL 1"	01	PÇ
306723	B3	TUBO ACO CARBONO GALVANIZADO A FOGO CLASSE PRESSAO MEDIA COM COSTURA LONGITUDINAL 6M (S/REBARBA INTERNA OXIDO ZINCO OLEO TAMPAS) ROSCA BSP POL 1"	0,15	m
311119	B4	VALVULA ESFERA TRIPARTIDA CORPO ESFERA ALAVANCA EM INOX 304/CF8 PASSAGEM PLENA VEDACAO PTFE PN 20 (CLASSE 300) ROSCA BSP POL 1"	01	PÇ
** 313349	B5	VENTOSA SIMPLES FUNCAO COM ROSCA BSP EM CORPO PLASTICO COM CAPACIDADE MINIMA DE VAZAO DE 25 M3/H A 4 BAR E DE 115 M3/H A 16 BAR PN 10/16 POL 1"	01	PÇ
MANÔMETRO E ESPERA P/ SENSOR DE PRESSÃO				
30880	C1	NIPLE FG BSP POL 1/2"	03	PÇ
31429	C2	TE FG BSP POL 1/2"	01	PÇ
302108	C3	VALVULA ESFERA TRIPARTIDA CORPO ESFERA ALAVANCA EM INOX 304 PASSAGEM PLENA VEDACAO PTFE PN25 (CLASSE 300) ROSCA BSP POL 1/2"	02	PÇ
77780	C4	NIPLE REDUCAO FG BSP POL 1/2" POL 1/4"	01	PÇ
30724	C5	LUVA FG BSP POL 1/4"	01	PÇ
319446	C6	MANOMETRO ANALOGICO ACO INOX 304 CAIXA 50/52MM IP 65 VISOR POLICARBONATO ENCHIMENTO GLICERINA MONTAGEM DIRETA VERTICAL INOX 1000KGF/CM2 BSP 1/4 POL	01	PÇ
ACESSÓRIOS PARA FLANGES				
ACESSÓRIOS PARA FLANGES DE SUPERFÍCIE				
326621	S/N	KIT PARAFUSO PORCA ARRUELA LISA ACO CARBONO ARRUELA VEDACAO FURACAO PN 10 NBR 7675 DN 50	02	PÇ

* VER ESPECIFICAÇÃO TÉCNICA.
** VER ESPECIFICAÇÃO BÁSICA CÓDIGOS SAM.

NOTAS

01 – DIMENSÕES EM CENTÍMETROS E ELEVAÇÕES EM METROS, EXCETO ONDE INDICADO.

02 – CONFIRMAR A POSIÇÃO E A PROFUNDIDADE DAS TUBULAÇÕES EXISTENTES NA OBRA.

03 – OS DANOS CAUSADOS ÀS INSTALAÇÕES SUBTERRÂNEAS SERÃO DE INTEIRA RESPONSABILIDADE DA EXECUTORA DAS OBRAS, INDEPENDENTEMENTE DA INTERFERÊNCIA CONSTAR OU NÃO NOS DESENHOS.

04 – O PROJETO BÁSICO HIDRÁULICO FOI COMPATIBILIZADO COM OS DEMAIS PROJETOS CONTRATADOS, CONFORME AS ESPECIALIDADES LISTADAS ABAIXO.

PROJETO/SERVIÇO	DESENVOLVIMENTO
BÁSICO HIDRÁULICO	S.J.M.H. ENGENHARIA E CONSTRUÇÕES LTDA.
TOPOGRAFIA	SOCIEDADE DA ÁGUA SERVIÇOES AMBIENTAIS E GEOTECNOLOGIAS
BÁSICO ELÉTRICO/AUTOMAÇÃO	S.J.M.H. ENGENHARIA E CONSTRUÇÕES LTDA.
BÁSICO MECÂNICO/ESPECIFICAÇÕES	S.J.M.H. ENGENHARIA E CONSTRUÇÕES LTDA.
SONDAGENS SPT	GEOLOC LOCAÇÕES E SONDAGENS LTDA.
BÁSICO ESTRUTURAL	S.J.M.H. ENGENHARIA E CONSTRUÇÕES LTDA.
BÁSICO GEOTÉCNICO	S.J.M.H. ENGENHARIA E CONSTRUÇÕES LTDA.

SANEPAR Companhia de Saneamento do Paraná

MUNICÍPIO/SISTEMA:
GENERAL CARNEIRO - JANGADA DO SUL
SISTEMA DE ABASTECIMENTO DE ÁGUA

BLOCO Nº: FOLHA Nº:
01 - 03/09

PROJETO/UNIDADE CONSTRUTIVA:
PROJETO BÁSICO HIDRÁULICO
CAPTAÇÃO SUBTERRÂNEA - CSB-01 / EEB-01
PLANTA, CORTE A1 E DETALHES

DATA: AGOSTO/2023

ESCALA: INDICADA

GERÊNCIA DA SANEPAR
GPOSD
Gerência Projetos e Obras Sudeste
R. Monte Alverne nº644 - Jardim Carvalho - CEP 84036-010 - Ponta Grossa - PR
GERENTE: JOEL PIRES CREA Nº: 100.276 - D/PR
COORDENADOR GERAL DO PROJETO: DENIS SCHECHTEL NEVES CRQ 09450611/PR
FISCALIZAÇÃO DO PROJETO CIVIL E HIDRÁULICO: DIOGENES VERGES 78.132 - D/PR
FISCALIZAÇÃO DO PROJETO ELÉTRICO, AUTOMAÇÃO E INSTRUMENTAÇÃO: DIOGENES VERGES 78.132 - D/PR
FISCALIZAÇÃO DO PROJETO MECÂNICO: ARTHUR VIEIRA NETO 107.842 - D/PR
FISCALIZAÇÃO DO PROJ. ELÉTRICO E AUTOM.: -
FISCALIZAÇÃO DO PROJ. UNIDADES LINEARES: -
DESENVOLVIMENTO DO DESENHO: -
ADEQUAÇÃO DO DESENHO: - -

EMPRESA CONTRATADA
S.J.M.H. Engenharia e Construções Ltda.
R. Marechal Deodoro nº556, Sala 104 - CEP 80010-010 - Curitiba/PR - e-mail: sjmh@sjmh.com.br
RESP. TÉCNICO DO PROJETO: SONS JON SCREMIN CREA Nº: 166.833 - D/PR
RESP. TÉCNICO DO PROJETO: -- CREA Nº: --
ARQUIVO ELETRÔNICO: 003-SAA-0674-9142-PBHI-DE-0000CSB01DETALHAMENTO-R0

A1 NORMAL – SJMH