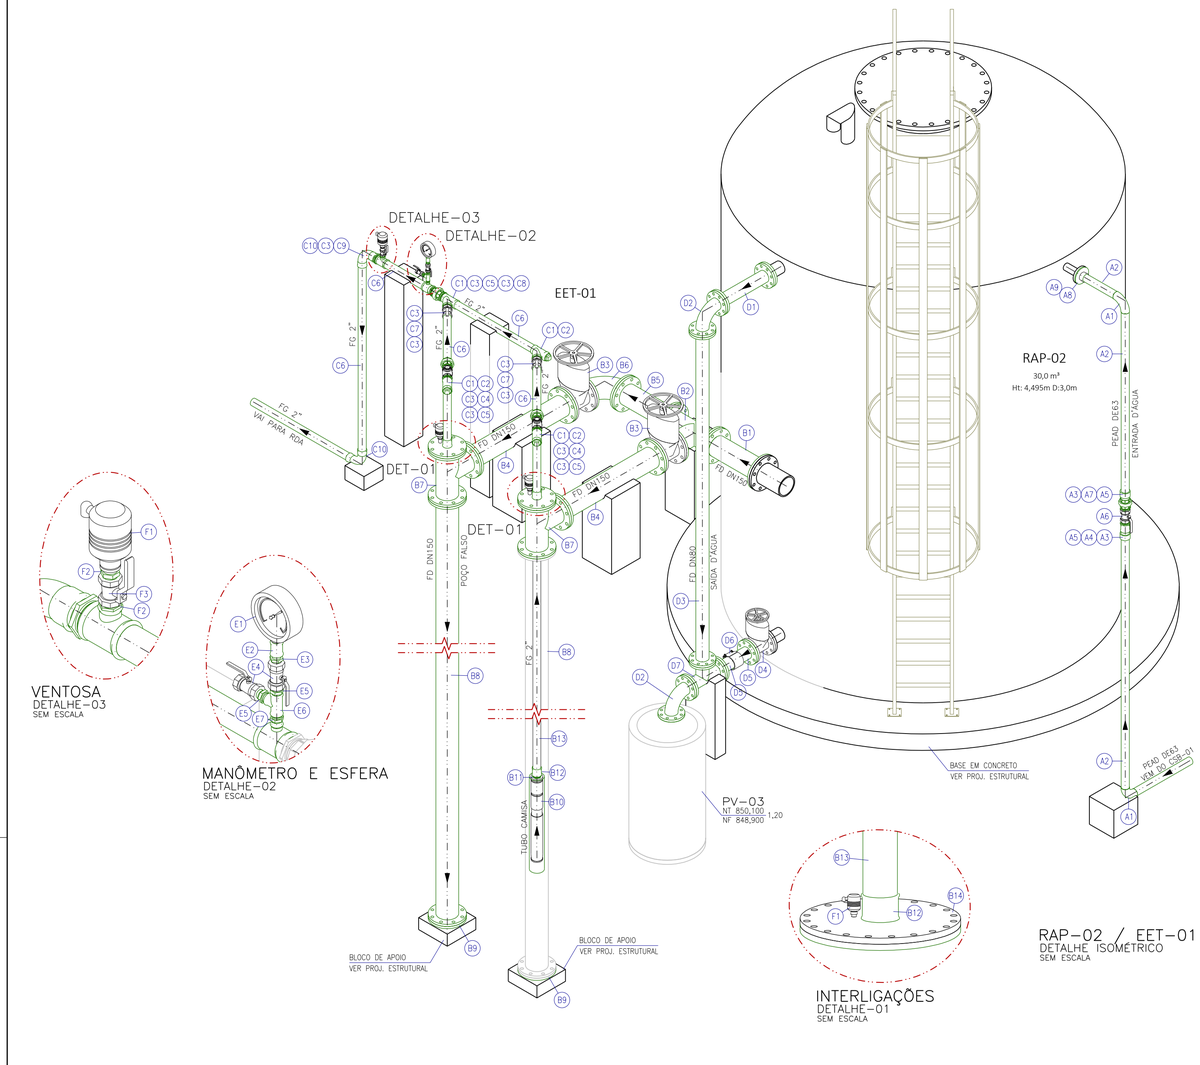


MANÔMETRO E ESFERA

319446	E1	MANOMETRO ANALOGICO ACO INOX 304 CAIXA 50/52MM IP 65 VISOR POLICARBONATO ENCHIMENTO GLICERINA MONTAGEM DIRETA VERTICAL INOX 160 MCA BSP 1/4 POL	01	PÇ
30724	E2	LUVA FG BSP POL 1/4"	01	PÇ
77780	E3	NIPLE REDUCAO FG BSP POL 1/2" POL 1/4"	01	PÇ
302108	E4	VALVULA ESFERA TRIPARTIDA CORPO ESFERA ALAVANCA EM INOX 304 PASSAGEM PLENA VEDACAO PTFE PN25 (CLASSE 300) ROSCA BSP POL 1/2"	02	PÇ
30880	E5	NIPLE FG BSP POL 1/2"	02	PÇ
31429	E6	TE FG BSP POL 1/2"	01	PÇ
139343	E7	NIPLE REDUCAO FG BSP POL 3/4" POL 1/2"	01	PÇ


VENTOSA

** 300125	F1	VENTOSA SIMPLES FUNCAO COM ROSCA BSP EM CORPO PLASTICO COM CAPACIDADE MINIMA DE VAZAO DE 25 M3/H A 4 BAR E DE 115 M3/H A 16 BAR PN 10/16 POL 3/4"	03	PÇ
30899	F2	NIPLE FG BSP POL 3/4"	02	PÇ
302109	F3	VALVULA ESFERA TRIPARTIDA CORPO ESFERA ALAVANCA EM INOX 304/CF8 PASSAGEM PLENA VEDACAO PTFE PN 20 (CLASSE 300) ROSCA BSP POL 3/4"	01	PÇ


ACESSÓRIOS PARA CONEXÕES FLANGEADAS

326621	S/N	KIT PARAFUSO PORCA ARRUELA LISA ACO CARBONO ARRUELA VEDACAO FURACAO PN 10 NBR 7675 DN 50	01	PÇ
326622	S/N	KIT PARAFUSO PORCA ARRUELA LISA ACO CARBONO ARRUELA VEDACAO FURACAO PN 10 NBR 7675 DN 80	05	PÇ
326624	S/N	KIT PARAFUSO PORCA ARRUELA LISA ACO CARBONO ARRUELA VEDACAO FURACAO PN 10 NBR 7675 DN 150	11	PÇ

* VER ESPECIFICAÇÃO TÉCNICA.
** VER ESPECIFICAÇÃO BÁSICA CÓDIGOS SAM.

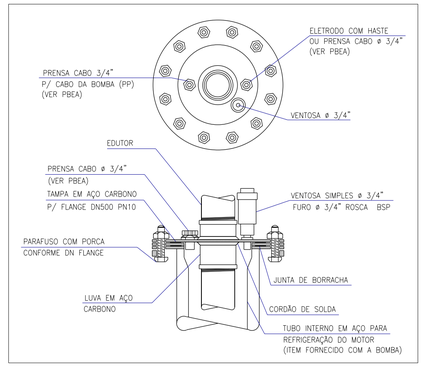


TAMPA DO POÇO FALSO
DETALHE
SEM ESCALA

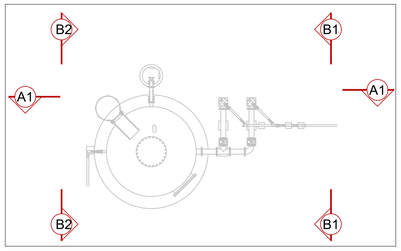

RELAÇÃO DE EQUIP. E MATERIAIS

NOVO PÁTIO DE RESERVAÇÃO E TRATAMENTO

COD.	Nº	DISCRIMINAÇÃO	QT.	UN.
RAP-02				
** 311393	S/N	RESERVATORIO VERTICAL BASE APOIADA EM MATERIAL PRFV OU ACO INOXIDAVEL CAPACIDADE 30 M3 D: 3,00 m V: 30,0 m3	01	UN.
ALIMENTAÇÃO RAP-02				
309982	A1	CURVA POLIETILENO INJETADA 90 TERMOFUSAO PE 100 PN10 DE 63	02	PÇ
298739	A2	TUBO POLIETILENO PE 100 PN10 (BARRA COM 6,0 M) DE 63	5,0	m
303132	A3	ADAPTADOR DE TRANSICAO PEAD/PP/PLAST.ENG. BB JUNTA DE COMPRESSAO/ROSCA BSP FEMEA ACESSORIOS ACO INOX 304 PVC NBR 5647 PEAD NBR 15561 PN16 DE 63 POL 2"	02	PÇ
30791	A4	LUVA FG BSP POL 2"	01	PÇ
30937	A5	NIPLE FG BSP POL 2"	02	PÇ
302113	A6	VALVULA ESFERA TRIPARTIDA CORPO ESFERA ALAVANCA EM INOX 304/CF8PASSAGEM PLENA VEDACAO PTFE PN 20 (CLASSE 300) ROSCA BSP POL 2"	01	PÇ
134880	A7	UNIAO FG ASSENTO CONICO BRONZE BSP POL 2"	01	PÇ
175226	A8	FLANGE ACO CARBONO PARA COLARINHO PEAD EPOXI ISO 12944 320UM C5M DURABILIDADE ALTA OU PP (NBR 7675/15593) PN10 DE 63 DN50	01	PÇ
309898	A9	COLARINHO POLIETILENO INJETADO TERMOFUSAO PE 100 PN10 DE 63	01	PÇ
BARRILETE DE SUCÇÃO – EET-01				
282680	B1	TOCO DE TUBO FD FF PN10 MEDINDO 0,50M DN150	01	PÇ
302842	B2	TE FD FFF PN10 DN150	01	PÇ
299850	B3	REGISTRO GAVETA FD COM CUNHA ELASTICA E VOLANTE FF SERIE 14 CORPO CURTO PN10 DN150	02	PÇ
316671	B4	TUBO FD K9 FF (SOLDA INTERFERENCIA) PN10 MEDINDO 1,00M DN150	02	PÇ
282680	B5	TOCO DE TUBO FD FF PN10 MEDINDO 0,50M DN150	01	PÇ
299699	B6	CURVA FD FF 90 PN10 DN150	01	PÇ
302842	B7	TE FD FFF PN10 DN150	02	PÇ
283956	B8	TUBO FD K9 FF (SOLDA INTERFERENCIA) PN10 MEDINDO 5,80M DN150	02	PÇ
307951	B9	FLANGE FD CEGO COM FURACAO PN10 DN150	02	PÇ
* –	B10	MOTOBOMBA SUBMERSA Q: 7,0 m3/h Hm: 55,0 mca	01+01P	PÇ
–		TUBO CAMISA NA SUCÇÃO – FORNECIDO COM A BOMBA (30cm A CIMA DO FUNDO)	02	PÇ
30937	B11	NIPLE FG BSP POL 2"	02	PÇ
30791	B12	LUVA FG BSP POL 2"	02	PÇ
306726	B13	TUBO ACO CARBONO GALVANIZADO A FOGO CLASSE PRESSAO MEDIA COM COSTURA LONGITUDINAL 6M (S/REBARBA INTERNA OXIDO ZINCO OLEO TAMPAS) ROSCA BSP POL 4"	2X 6,0	m
299956	B14	TAMPA SANITARIA PARA POCO TUBULAR PROFUNDO 6 X 2 POL	02	PÇ
BARRILETE DE RECALQUE – EET-01				
31470	C1	TE FG BSP POL 2"	04	PÇ
31046	C2	BUJAO (PLUG) FG POL BSP POL 2"	03	PÇ
30937	C3	NIPLE FG BSP POL 2"	10	PÇ
140600	C4	VALVULA RETENCAO BRONZE VERTICAL PN16 BSP POL 2"	02	PÇ
134880	C5	UNIAO FG ASSENTO CONICO BRONZE BSP POL 2"	03	PÇ
306724	C6	TUBO ACO CARBONO GALVANIZADO A FOGO CLASSE PRESSAO MEDIA COM COSTURA LONGITUDINAL 6M (S/REBARBA INTERNA OXIDO ZINCO OLEO TAMPAS) ROSCA BSP POL 2"	4,0	m
302113	C7	VALVULA ESFERA TRIPARTIDA CORPO ESFERA ALAVANCA EM INOX 304/CF8PASSAGEM PLENA VEDACAO PTFE PN 20 (CLASSE 300) ROSCA BSP POL 2"	02	PÇ
31666	C8	TE REDUCAO FG BSP POL 2" POL 1/2"	01	PÇ
31674	C9	TE REDUCAO FG BSP POL 2" POL 3/4"	01	PÇ
134163	C10	CURVA FG FEMEA/FEMEA 90° BSP POL 2"	01	PÇ
EXTRAVASOR E DESCARGA – RAP-02				
7013	D1	TOCO DE TUBO FD FF PN10 MEDINDO 0,50 METROS DN80	01	PÇ
57762	D2	CURVA FD FF 90 PN10 DN80	02	PÇ
317082	D3	TUBO FD K9 FF (SOLDA INTERFERENCIA) PN10 MEDINDO 3,00M DN80	01	PÇ
311847	D4	REGISTRO GAVETA FD COM CUNHA ELASTICA E VOLANTE FF SERIE 14 CORPO CURTO PN10 DN80	01	PÇ
305862	D5	TUBO FD PF PN10 MEDIDAS DE 0,36 ATE 0,50 METROS DN80 (L:0,17m) AJUSTAR NO LOCAL	02	PÇ
314336	D6	CINTA DE VEDACAO COM GRIP ACO INOX 304 ANEL VEDACAO EPDM ISO 19921 PN 16 PARA TUBO FD DE 98 DN 80	01	PÇ
12734	D7	TE FD FFF PN10 DN80	01	PÇ

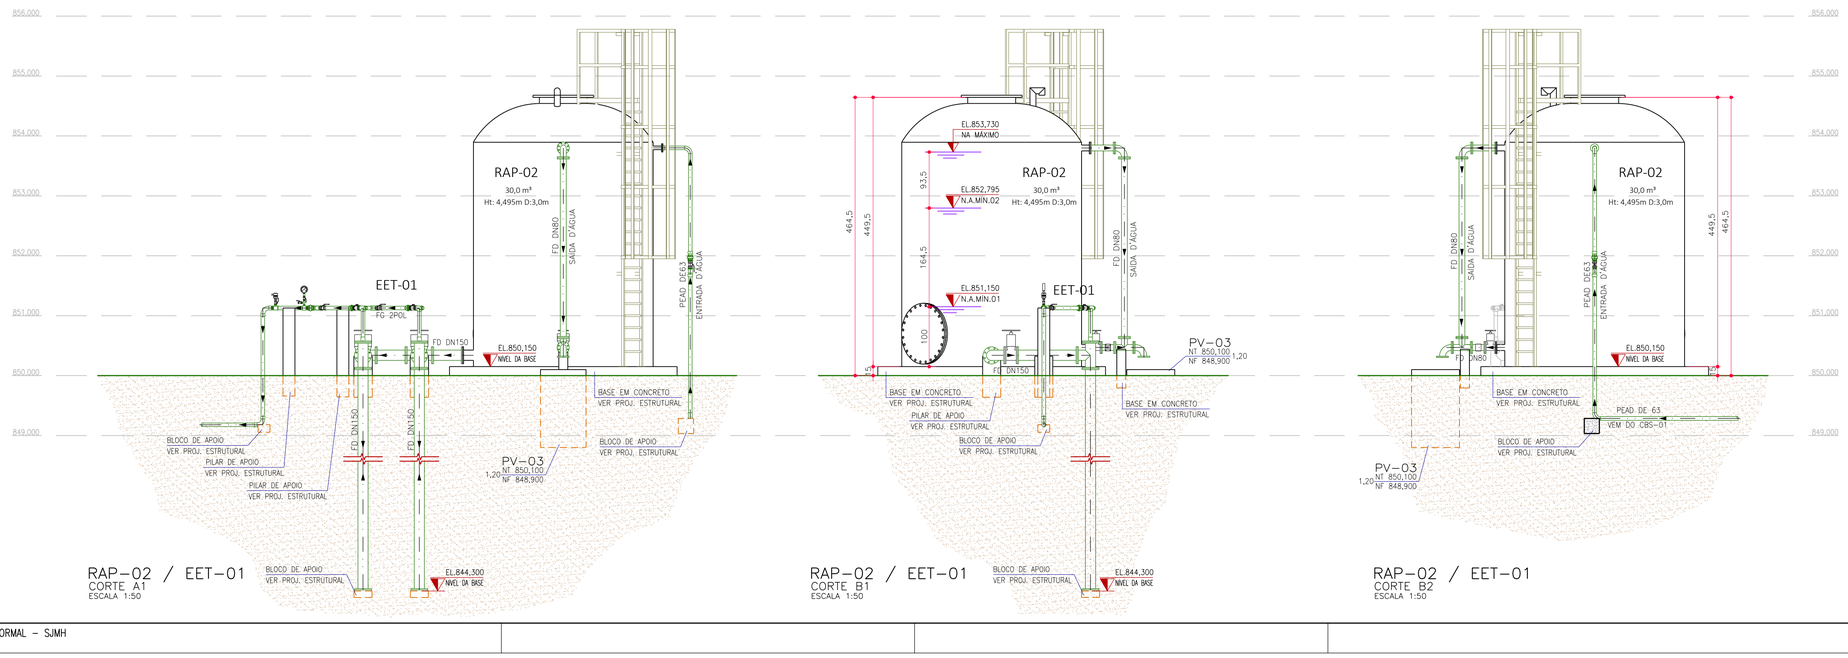

RAP-02 / EET-01
CORTE A1
ESCALA 1:50

RAP-02 / EET-01
CORTE B1
ESCALA 1:50

RAP-02 / EET-01
CORTE B2
ESCALA 1:50

NOTAS

01 – DIMENSÕES EM CENTÍMETROS E ELEVAÇÕES EM METROS, EXCETO ONDE INDICADO.

02 – CONFIRMAR A POSIÇÃO E A PROFUNDIDADE DAS TUBULAÇÕES EXISTENTES NA OBRA.

03 – OS DANOS CAUSADOS ÀS INSTALAÇÕES SUBTERRÂNEAS SERÃO DE INTEIRA RESPONSABILIDADE DA EXECUTORA DAS OBRAS, INDEPENDENTEMENTE DA INTERFERÊNCIA CONSTAR OU NÃO NOS DESENHOS.

04 – O PROJETO BÁSICO HIDRÁULICO FOI COMPATIBILIZADO COM OS DEMAIS PROJETOS CONTRATADOS, CONFORME AS ESPECIALIDADES LISTADAS ABAIXO.

PROJETO/SERVIÇO	DESENVOLVIMENTO
BÁSICO HIDRÁULICO	S.J.M.H. ENGENHARIA E CONSTRUÇÕES LTDA.
TOPOGRAFIA	SOCIEDADE DA ÁGUA SERVIÇOES AMBIENTAIS E GEOTECNOLOGIAS
BÁSICO ELÉTRICO/AUTOMAÇÃO	S.J.M.H. ENGENHARIA E CONSTRUÇÕES LTDA.
BÁSICO MECÂNICO/ESPECIFICAÇÕES	S.J.M.H. ENGENHARIA E CONSTRUÇÕES LTDA.
SONDAGENS SPT	GEOLOC LOCAÇÕES E SONDAGENS LTDA.
BÁSICO ESTRUTURAL	S.J.M.H. ENGENHARIA E CONSTRUÇÕES LTDA.
BÁSICO GEOTÉCNICO	S.J.M.H. ENGENHARIA E CONSTRUÇÕES LTDA.

SANEPAR Companhia de Saneamento do Paraná

MUNICÍPIO/SISTEMA:
GENERAL CARNEIRO - JANGADA DO SUL
SISTEMA DE ABASTECIMENTO DE ÁGUA

BLOCO Nº: FOLHA Nº:
01 - 04/09

PROJETO/UNIDADE CONSTRUTIVA:
PROJETO BÁSICO HIDRÁULICO
ELEVATÓRIA E RESERVATÓRIO - EET-01 / RAP-02
CORTES E DETALHES

DATA: AGOSTO/2023

ESCALA: INDICADA

GERÊNCIA DA SANEPAR
GPOSD
Gerência Projetos e Obras Sudeste
R. Monte Alverne nº644 - Jardim Carvalho - CEP 84036-010 - Ponta Grossa - PR
GERENTE: JOEL PIRES CREA Nº: 100.276 - D/PR

COORDENADOR GERAL DO PROJETO: DENIS SCHECHTEL NEVES CREA 094026/7/PR	FISCALIZAÇÃO DO PROJ. ELETRICO E AUTOM.: -
FISCALIZAÇÃO DO PROJETO CIVIL/HIDRÁULICO: DIOGENES VERGES 78.132 - D/PR	FISCALIZAÇÃO DO PROJ. UNIDADES LINEARES: -
FISCALIZAÇÃO PROJ. ESTRUT. GEOTEC. SONG.: DIOGENES VERGES 78.132 - D/PR	DESENVOLVIMENTO DO DESENHO: -
FISCALIZAÇÃO DO PROJETO MECÂNICO: ARTHUR VIEIRA NETO 107.842 - D/PR	ADEQUAÇÃO DO DESENHO: -

EMPRESA CONTRATADA
S.J.M.H.
S.J.M.H. Engenharia e Construções Ltda.
R. Marechal Deodoro nº530, Sala 164 - CEP 80010-010 - Curitiba/PR - e-mail: sjmh@sjmh.com.br

RESP. TÉCNICO DO PROJETO: SONG JON SCREMIN CREA Nº: 166.833 - D/PR	RESP. TÉCNICO DO PROJETO: -- CREA Nº: --
ARQUIVO ELETRÔNICO: 004-SAA-0674-9142-PBHI-DE-0000EET01DETALHAMENTO-R0	

A1 NORMAL – SJMH