
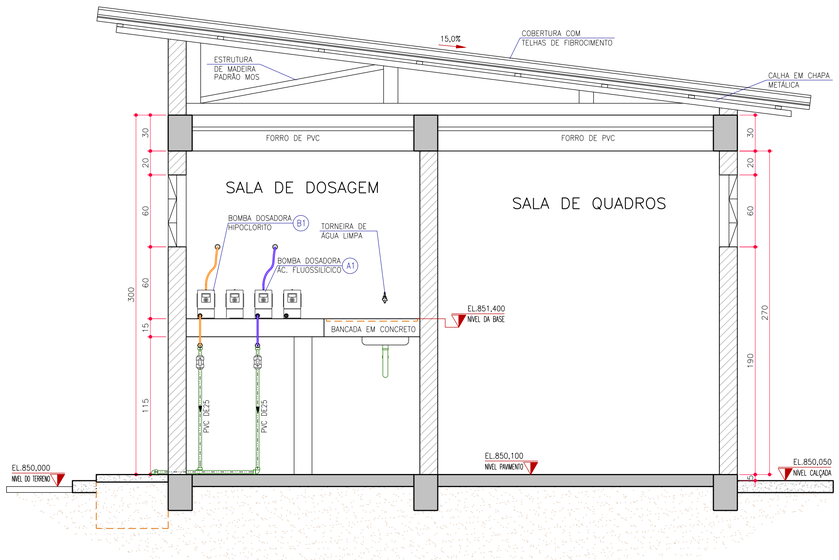


CASA DE QUÍMICA
CORTE A1
ESCALA 1:25

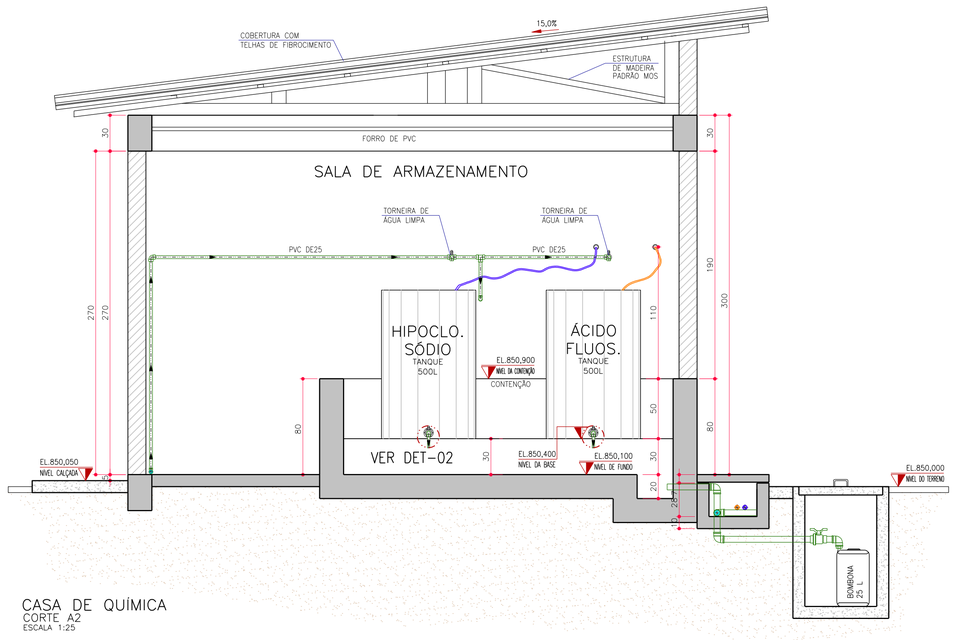


CASA DE QUÍMICA
CORTE A2
ESCALA 1:25


RELAÇÃO DE EQUIP. E MATERIAIS

SCF-01 – CASA DE QUÍMICA


	COD.	Nº	DISCRIMINAÇÃO	QT.	UN.
			INTERLIGAÇÕES – ÁCIDO FLUOSSILÍCICO		
**	310139	A1	BOMBA DOSADORA DIAFRAGMA PASSO OU PERISTALTICA PROD QUIM EXCETO HIDRÓX CALCIO CARVAO COM AUTOMACAO 4 A 20MA E DISPLAY TIPO 2B 7L/H 15BAR	02	PÇ
	300907	A2	REDUCAO PVC SCH80 JS PN10 DE40 X 25MM ASTM D2467 NSF/ANSI STD 14&61 FDA 21	01	PÇ
	301259	A3	JOELHO PVC JS 90 SCH80 PN10 DE25MM ASTM D2467 NSF/ANSI STD 14&61 FDA 21	04	PÇ
	300889	A4	TUBO PVC SCH80 JS PN10 DE25MM ASTM D1785 NSF/ANSI STD 14&61 FDA 21	2,5	m
	301427	A5	VALVULA ESFERA DUPLA UNIAO PVC JS BB SCH80 ACIONAMENTO MANUAL POR VOLANTE EN ISO 16135 (ASTM D1785/D2467) NSF/ANSI STD14/61 FDA 21 POL 3/4"	01	PÇ
			INTERLIGAÇÕES DE APLICAÇÃO – HIPOCLORITO DE SÓDIO		
**	310143	B1	BOMBA DOSADORA DIAFRAGMA PASSO OU PERISTALTICA PROD QUIM EXCETO HIDRÓX CALCIO CARVAO COM AUTOMACAO 4 A 20MA E DISPLAY TIPO 2B 12L/H 10BAR	02	PÇ
	300408	B2	REDUCAO CPVC SCH80 JS PN10 ASTM F439 NSF/ANSI STD 14&61 FDA 21 DE 40 DE 25	01	PÇ
	300490	B3	CURVA CPVC JS BB 90 PN10 SCHEDULE 80 ASTM F439 NSF/ANSI STD 14&61 FDA 21 DE 25	05	PÇ
	300385	B4	TUBO CPVC SCH80 SOLDAVEL PN10 P/ TUBULACAO DE25MM ASTM F441 NSF/ANSI STD 14&61 FDA 21 DE 25	2,5	m
	300590	B5	VALVULA ESFERA DUPLA UNIAO CPVC JS BB SCH80 ACIONAMENTO MANUAL POR VOLANTE EN ISO 16135 (ASTM F441/F439) NSF/ANSI STD14/61 FDA 21 POL 3/4"	01	PÇ
			DESCARGA DE FUNDO		
	309111	C1	ADAPTADOR PVC JS BOLSA/ROSCA MACHO BSP SCH80 PN10 ASTM D2467 NSF/ANSI STD 14&61 FDA 21 DE 50 POL 1.1/2"	03	PÇ
	300909	C2	REDUCAO PVC JS BB SCH80 ASTM D2467 NSF/ANSI STD14/61 FDA 21 POL 1.1/2" POL 1/2"	03	PÇ
	301317	C3	NIPLE ROSCA NPT MACHO/ROSCA NPT MACHO PVC SCH80 JS PN10 1/2 POL ASTM D2467 NSF/ANSI STD 14&61 FDA 21	06	PÇ
	301426	C4	VALVULA ESFERA DUPLA UNIAO PVC JS BB SCH80 ACIONAMENTO MANUAL POR VOLANTE EN ISO 16135 (ASTM D1785/D2467) NSF/ANSI STD14/61 FDA 21 POL 1/2"	03	PÇ
	301258	C5	JOELHO PVC JS 90 SCH80 PN10 DE20MM ASTM D2467 NSF/ANSI STD 14&61 FDA 21	03	PÇ
	300888	C6	TUBO PVC SCH80 JS PN10 DE20MM ASTM D1785 NSF/ANSI STD 14&61 FDA 21	0,5	m
**	309260	S/N	RESERVATORIO EM POLIETILENO PARA PRODUTO QUIMICO OU AGUA COM TAMPA DE SOBREPOR 500L	02	PÇ

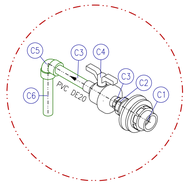

DETALHE-02
CONEXÕES
SEM ESCALA

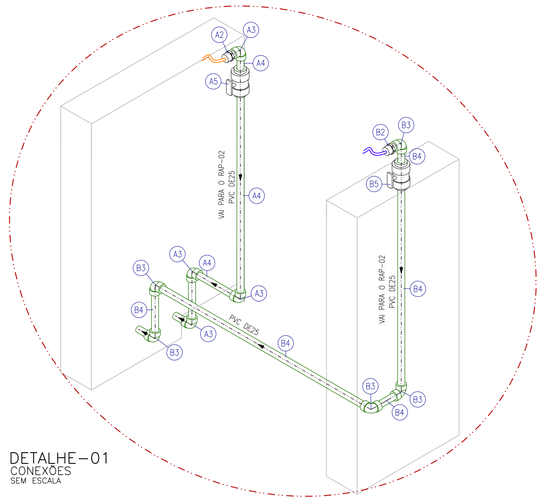

DETALHE-01
CONEXÕES
SEM ESCALA

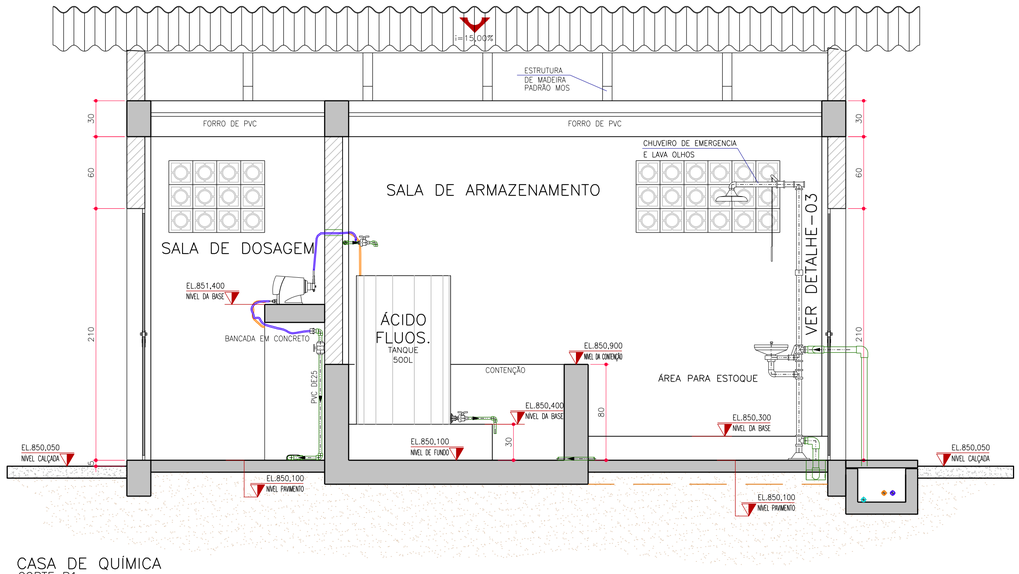

CASA DE QUÍMICA
CORTE B1
ESCALA 1:25

NOTAS

01 – DIMENSÕES EM CENTÍMETROS E ELEVAÇÕES EM METROS, EXCETO ONDE INDICADO.

02 – CONFIRMAR A POSIÇÃO E A PROFUNDIDADE DAS TUBULAÇÕES EXISTENTES NA OBRA.

03 – OS DANOS CAUSADOS ÀS INSTALAÇÕES SUBTERRÂNEAS SERÃO DE INTEIRA RESPONSABILIDADE DA EXECUTORA DAS OBRAS, INDEPENDENTEMENTE DA INTERFERÊNCIA CONSTAR OU NÃO NOS DESENHOS.

04 – O PROJETO BÁSICO HIDRÁULICO FOI COMPATIBILIZADO COM OS DEMAIS PROJETOS CONTRATADOS, CONFORME AS ESPECIALIDADES LISTADAS ABAIXO.

PROJETO/SERVIÇO	DESENVOLVIMENTO
BÁSICO HIDRÁULICO	S.J.M.H. ENGENHARIA E CONSTRUÇÕES LTDA.
TOPOGRAFIA	SOCIEDADE DA ÁGUA SERVIÇOES AMBIENTAIS E GEOTECNOLOGIAS
BÁSICO ELÉTRICO/AUTOMAÇÃO	S.J.M.H. ENGENHARIA E CONSTRUÇÕES LTDA.
BÁSICO MECÂNICO/ESPECIFICAÇÕES	S.J.M.H. ENGENHARIA E CONSTRUÇÕES LTDA.
SONDAGENS SPT	GEOLOC LOCAÇÕES E SONDAGENS LTDA.
BÁSICO ESTRUTURAL	S.J.M.H. ENGENHARIA E CONSTRUÇÕES LTDA.
BÁSICO GEOTÉCNICO	S.J.M.H. ENGENHARIA E CONSTRUÇÕES LTDA.

SANEPAR Companhia de Saneamento do Paraná

MUNICÍPIO/SISTEMA:
GENERAL CARNEIRO - JANGADA DO SUL
SISTEMA DE ABASTECIMENTO DE ÁGUA

BLOCO Nº: FOLHA Nº: 01 - 06/09

PROJETO/UNIDADE CONSTRUTIVA:
PROJETO BÁSICO HIDRÁULICO
CASA DE QUÍMICA - SCF-01
CORTES E DETALHES

DATA: AGOSTO/2023

ESCALA: INDICADA

GERÊNCIA DA SANEPAR:
GPOSD
Gerência Projetos e Obras Sudeste
R. Monte Alverne nº644 - Jardim Carvalho - CEP 84016-010 - Ponta Grossa - PR
GERENTE: JOEL PIRES CREA Nº: 100.276 - D/PR

EMPRESA CONTRATADA:
S.J.M.H. Engenharia e Construções Ltda.
R. Marechal Deodoro nº300, Sala 194 - CEP 80010-010 - Curitiba-PR - e-mail: sjmh@sjmh.com.br

COORDENADOR GERAL DO PROJETO: DENIS SCHECHTEL NEVES - CRQ 09402617/PR	FISCALIZAÇÃO DO PROJ. ELÉTRICO E AUTOM.: -
FISCALIZAÇÃO DO PROJETO CIVIL/HIDRÁULICO: DIOGENES VERGES - 78.132 - D/PR	FISCALIZAÇÃO DO PROJ. UNIDADES LINEARES: -
FISCALIZAÇÃO PROJ. ESTRUT., GEOTEC. SONDAG.: DIOGENES VERGES - 78.132 - D/PR	DESENVOLVIMENTO DO DESENHO: -
FISCALIZAÇÃO DO PROJETO MECÂNICO: ARTHUR VIEIRA NETO - 107.842 - D/PR	ADEQUAÇÃO DO DESENHO: -

RESP. TÉCNICO DO PROJETO: SONG JON SCREMIN CREA Nº: 166.833 - D/PR

RESP. TÉCNICO DO PROJETO: -- CREA Nº: --

ARQUIVO ELETRÔNICO: 006-SAA-0674-9142-PBHI-DE-0000SCF01DETALHAMENTO-R0