

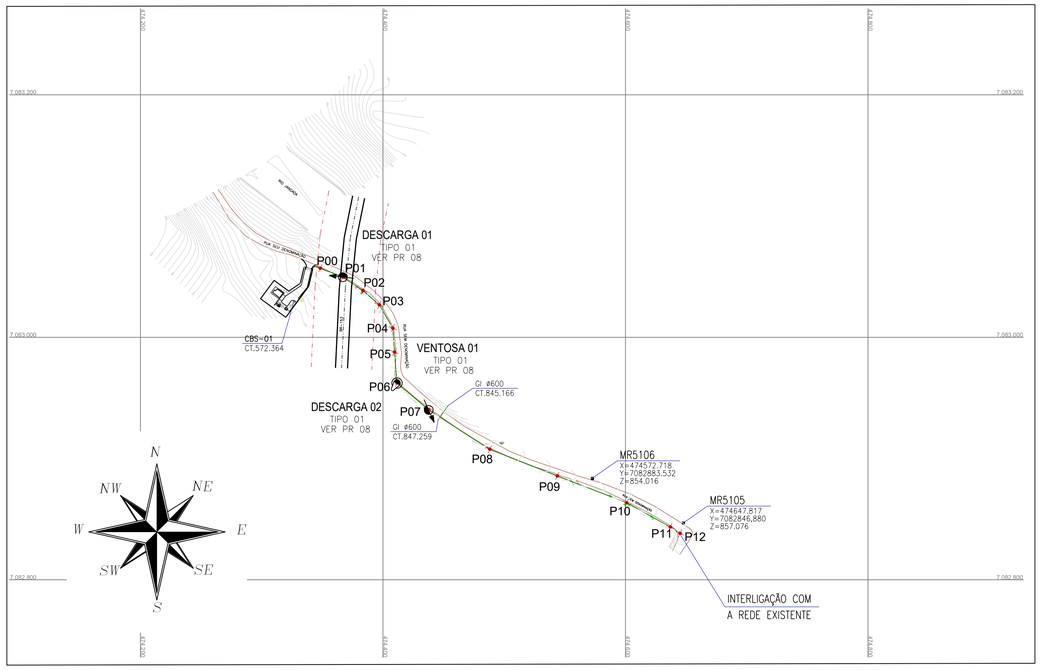


ESCALA HORIZONTAL 1:2000
ESCALA VERTICAL 1:200

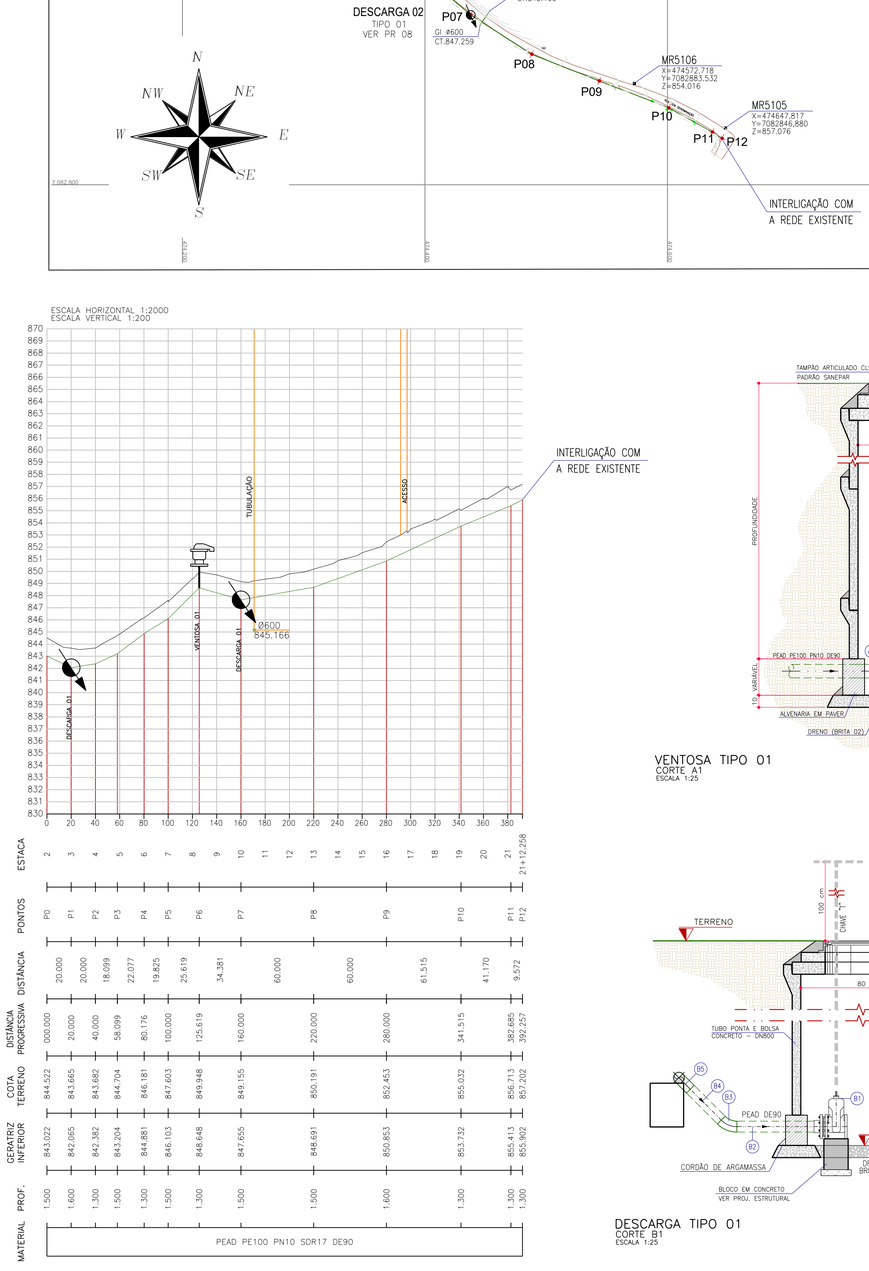


ADUTORA DE ÁGUA TRATADA – AAT–01
PLANTA E PERFIL LONGITUDINAL – PARTE 1
ESCALA HOR 1:2000 – ESCALA VER 1:200

VENTOSA TIPO 01
CORTE A1
ESCALA 1:25

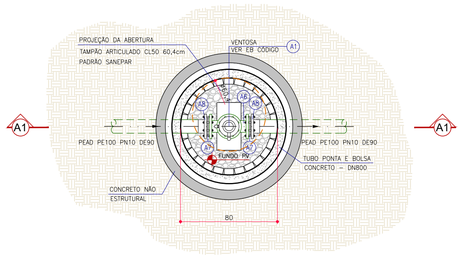

VENTOSA TIPO 01
PLANTA
ESCALA 1:25

DESCARGA TIPO 01
CORTE B1
ESCALA 1:25

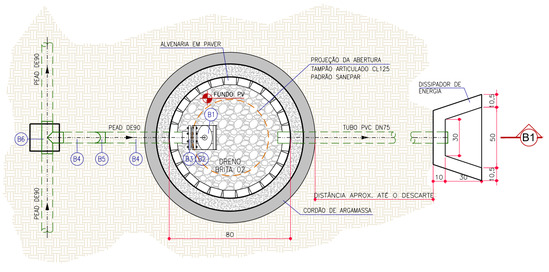

DESCARGA TIPO 01
PLANTA
ESCALA 1:25

VENTOSAS

N°	PONTO	G.I.E. (m)	TERRENO (m)	PROF. (m)	FUNDO PV (m)	DN	TIPO
01	P–06	848.648	849.155	1.300	848.548	2POL	01

DESCARGAS

N°	PONTO	G.I.E. (m)	TERRENO (m)	PROF. (m)	FUNDO PV (m)	DN	DITÂNCIA ATÉ O DESCARTE	TIPO
01	P–01	842.065	843.665	1.600	841.965	DN75	05 m	01
02	P–07	847.655	849.155	1.500	847.555	DN75	05 m	01

RELAÇÃO DE EQUIPAMENTOS E MATERIAIS

ADUTORA DE ÁGUA TRATADA – AAT–01

	COD.	N°	DISCRIMINAÇÃO	QT.	UN.
			TUBOS E CONEXÕES		
	298741	S/N	TUBO POLIETILENO PE 100 PN10 (ROLO COM 50,0 M) DE 90	393,0	m
			VENTOSA TIPO 01 (POÇO DE VISITA PADRÃO MOS – TIPO C)		
**	323236	A1	VENTOSA COMBINADA CORPO EM NYLON REFORCADO COM FUNCIONAMENTO SUAVE PARA ABERTURA E FECHAMENTO ROSCA BSP POL 2" 1x	01	PÇ
	302113	A2	VALVULA ESFERA TRIPARTIDA CORPO ESFERA ALAVANCA EM INOX 304/CF8PASSAGEM PLENA VEDACAO PTFE PN 20 (CLASSE 300) ROSCA BSP POL 2" 1x	01	PÇ
	30937	A3	NIPLE FG BSP POL 2" 1x	01	PÇ
	30538	A4	FLANGE FG COM SEXTAVADO BSP POL 2" 1x	01	PÇ
	307202	A5	REDUCAO FD FF CONCENTRICA PN10 DN80 DN50 1x	01	PÇ
	12734	A6	TE FD FFF PN10 DN80 1x	01	PÇ
	309899	A7	COLARINHO POLIETILENO INJETADO TERMOFUSAO PE 100 PN10 DE 90 1x	02	PÇ
	286031	A8	FLANGE ACO CARBONO COM FURACAO PARA COLARINHO PEAD EPOXI ISO 12944 320UM C5M DURABILIDADE ALTA OU PP (NBR 7675/15593) PN10 DE 90 DN80 1x	02	PÇ
**	270350	S/N	TAMPAO FD CLASSE 50 PARA POCO DE VISITA PADRAO SANEPAR 1x	01	PÇ
			DESCARGA TIPO 01		
	280496	B1	REGISTRO GAVETA FD COM CUNHA ELASTICA E CABECOTE FF SERIE 14 CORPO CURTO PN10 DN80 2x	01	PÇ
	286031	B2	FLANGE ACO CARBONO COM FURACAO PARA COLARINHO PEAD EPOXI ISO 12944 320UM C5M DURABILIDADE ALTA OU PP (NBR 7675/15593) PN10 DE 90 DN80 2x	01	PÇ
	309899	B3	COLARINHO POLIETILENO INJETADO TERMOFUSAO PE 100 PN10 DE 90 2x	01	PÇ
	298741	B4	TUBO POLIETILENO PE 100 PN10 (ROLO COM 50,0 M) DE 90 2x	1,5	m
	312045	B5	CURVA POLIETILENO INJETADA 45 TERMOFUSAO PE 100 PN10 DE 90 2x	01	PÇ
	309616	B6	TE POLIETILENO INJETADO TERMOFUSAO PE 100 PN10 DE 90 2x	01	PÇ
	167770	S/N	TAMPAO FD CLASSE 125 KN 850/910MM PASSAGEM LIVRE ARTICULADA ARO/ABA BETUME PARA POCO VISITA GARANTIA 1 ANO LOGO PADRAO SANEPAR 2x	01	PÇ
	64831	S/N	TUBO PVC–U JEI/JS PB (DUPLA ATUACAO) PARA ESGOTO PREDIAL E AGUA PLUVIAL NBR 5688 SERIE NORMAL 6M DN75 2x	5,0	m

CONVENÇÕES:

PONTO
DESCARGA
VENTOSA EM PERFIL
VENTOSA EM PLANTA
ADUTORA DE ÁGUA BRUTA

NOTAS:

NOTA 01 – DIMENSÕES EM CENTÍMETROS E ELEVAÇÕES EM METROS, EXCETO ONDE INDICADO.
NOTA 02 – TODOS OS DIMENSIONAMENTOS DOS BLOCOS E DAS PEÇAS EM CONCRETO DEVERÃO SER CONFIRMADOS NO PROJETO ESTRUTURAL.
NOTA 03 – CONFIRMAR A POSIÇÃO E A PROFUNDIDADE DAS TUBULAÇÕES EXISTENTES NA OBRA.
NOTA 04 – OS DANOS CAUSADOS ÀS INSTALAÇÕES SUBTERRÂNEAS SERÃO DE INTEIRA RESPONSABILIDADE DA EXECUTORA DAS OBRAS, INDEPENDENTEMENTE DA INTERFERÊNCIA CONSTAR OU NÃO NOS DESENHOS.
NOTA 05 – REPOR E COMPACTAR OS LOCAIS ESCAVADOS COM MATERIAL APROPRIADO.
NOTA 06 – PROTEGER AS TUBULAÇÕES EM PEAD COM BORRACHA LENÇOL QUANDO ESTES ESTIVEREM LIGADAS À BLOCO DE ANCORAGEM.

PROJETO/SERVIÇO	DESENVOLVIMENTO
BÁSICO HIDRÁULICO	S.J.M.H. ENGENHARIA E CONSTRUÇÕES LTDA.
TOPOGRAFIA	SOCIEDADE DA ÁGUA SERVIÇOES AMBIENTAIS E GEOTECNOLOGIAS
BÁSICO ELÉTRICO/AUTOMAÇÃO	S.J.M.H. ENGENHARIA E CONSTRUÇÕES LTDA.
BÁSICO MECÂNICO/ESPECIFICAÇÕES	S.J.M.H. ENGENHARIA E CONSTRUÇÕES LTDA.
SONDAGENS SPT	GEOLOC LOCAÇÕES E SONDAGENS LTDA.
BÁSICO ESTRUTURAL	S.J.M.H. ENGENHARIA E CONSTRUÇÕES LTDA.
BÁSICO GEOTÉCNICO	S.J.M.H. ENGENHARIA E CONSTRUÇÕES LTDA.

Nº	DESCRIÇÃO DA REVISÃO	DATA	ADEQUAÇÃO	RESP. TÉCNICO
R1	REVISÃO DA LISTA DE MATERIAIS - CORREÇÃO DO CÓDIGO E MATERIAL DA ADUTORA	24/01/2026	SONG JON SCREMIN	SONG JON SCREMIN

SANEPAR Companhia de Saneamento do Paraná

MUNICÍPIO/SISTEMA:
GENERAL CARNEIRO - JANGADA DO SUL
SISTEMA DE ABASTECIMENTO DE ÁGUA

BLOCO Nº: 01 FOLHA Nº: 07/09

PROJETO/UNIDADE CONSTRUTIVA:
PROJETO BÁSICO HIDRÁULICO
ADUTORA DE ÁGUA TRATADA - AAT-01
PLANTA, PERFIL LONGITUDINAL, VENTOSAS E DESCARGAS

DATA: AGOSTO/2023

ESCALA: INDICADA

GERÊNCIA DA SANEPAR
GPOSD
Gerência Projetos e Obras Sudeste
R. Maria Alverne nº644 - Jardim Carvalho - CEP 84068-010 - Ponta Grossa - PR
GERENTE: JOEL PIRES CREA Nº: 100.276 - D/PR

COORDENAÇÃO GERAL DO PROJETO:	FISCALIZAÇÃO DO PROJ. ELÉTRICO E AUTOM.
DENIS SCHECHTEL NEVES CRQ 09402617/PR	
FISCALIZAÇÃO DO PROJETO CIVIL/ARQUITETÔ.	FISCALIZAÇÃO DO PROJ. UNIDADES LINEARES
DIOGENES VERGES 78.132 - D/PR	
FISCALIZAÇÃO PROJ. ESTRUT. GEOTEC. SOND.	DESENVOLVIMENTO DO DESENHO
DIOGENES VERGES 78.132 - D/PR	
FISCALIZAÇÃO DO PROJETO MECÂNICO	ADEQUAÇÃO DO DESENHO
ARTHUR VIEIRA NETO 107.842 - D/PR	-

EMPRESA CONTRATADA:
S.J.M.H. Engenharia e Construções Ltda.
R. Marechal Deodoro nº500, Sala 164 - CEP 80010-010 - Curitiba-PR - e-mail: sjmh@sjmh.com.br

RESP. TÉCNICO DO PROJETO:	RESP. TÉCNICO DO PROJETO:
SONG JON SCREMIN	--
CREA Nº: 166.833 - D/PR	CREA Nº: --

ARQUIVO ELETRÔNICO:
007-SAA-0674-9142-PBHI-DE-0000AAT01PLANTAPERF01-R0