

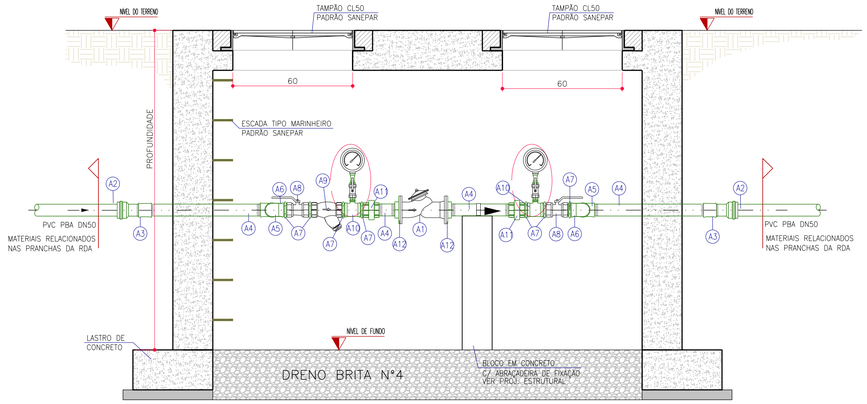



VÁLVULA REDUTORA DE PRESSÃO
CORTE A1
ESCALA 1:15

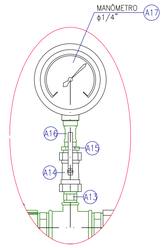

MANÔMETRO E ESPERA
DETALHE
SEM ESCALA

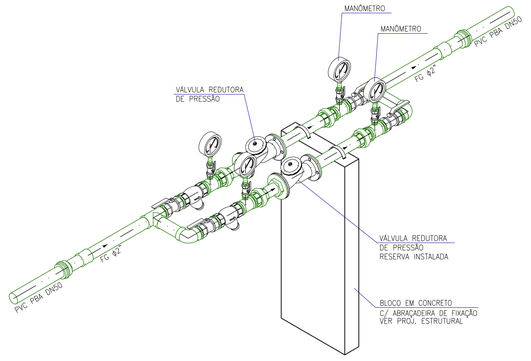

VRP DETALHE ISOMÉTRICO GERAL
DETALHE ILUSTRATIVA
SEM ESCALA

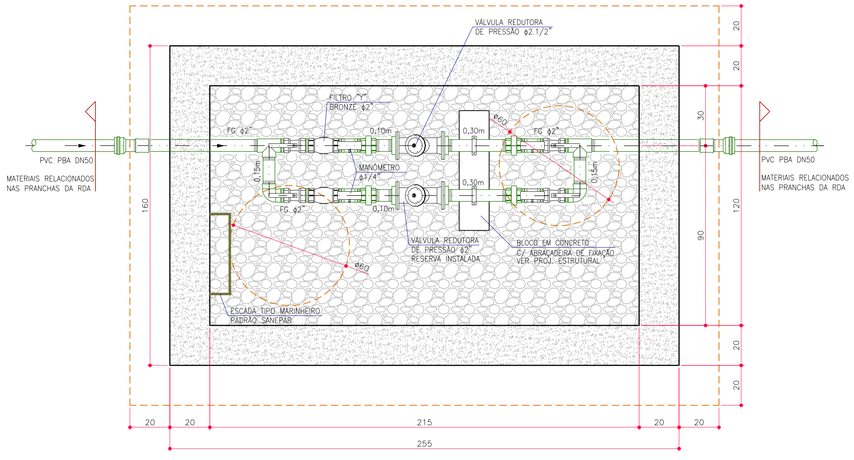

VÁLVULA REDUTORA DE PRESSÃO
PLANTA
ESCALA 1:15

RELAÇÃO DE EQUIPAMENTOS E MATERIAIS

	COD.	Nº	DISCRIMINAÇÃO	QT.	UN.
			VÁLVULA REDUTORA DE PRESSÃO		
**	179655	A1	VALVULA REDUTORA DE PRESSAO AUTO OPERADA PRESSAO DE ENTRADA ATE 10,0 BAR SAIDA AJUSTAVEL DE 1,0 A 3,0 BAR ROSCA BSP (2") OU FLANGE PN10 DN50	02	PÇ
	20117	A2	ADAPTADOR PVC JE BOLSA/ROSCA COM ANEL DN50 POL 2"	02	PÇ
	30791	A3	LUVA FG BSP POL 2"	02	PÇ
	306724	A4	TUBO ACO CARBONO GALVANIZADO A FOGO CLASSE PRESSAO MEDIA COM COSTURA LONGITUDINAL 6M (S/REBARBA INTERNA OXIDO ZINCO OLEO TAMPAS) ROSCA BSP POL 2"	2,50	m
	31470	A5	TE FG BSP POL 2"	02	PÇ
	29734	A6	COTOVELO FG BSP POL 2"	02	PÇ
	30937	A7	NIPLE FG BSP POL 2"	14	PÇ
	302113	A8	VALVULA ESFERA TRIPARTIDA CORPO ESFERA ALAVANCA EM INOX 304/CF8PASSAGEM PLENA VEDACAO PTFE PN 20 (CLASSE 300) ROSCA BSP POL 2"	04	PÇ
	35521	A9	FILTRO TIPO Y BRONZE OU FD OU ACO CARBONO PN10 COM TELA ACOINOX 304/316 0,8MM (AGUA FILTRADA) E BUJAO DE LIMPEZA ROSCADO VEDACAO TAMPA EPDM/TEFLON POL 2"	02	PÇ
	31666	A10	TE REDUCAO FG BSP POL 2" POL 1/2"	04	PÇ
	134880	A11	UNIAO FG ASSENTO CONICO BRONZE BSP POL 2"	04	PÇ
	30538	A12	FLANGE FG COM SEXTAVADO BSP POL 2"	04	PÇ
	30880	A13	NIPLE FG BSP POL 1/2"	04	PÇ
	302108	A14	VALVULA ESFERA TRIPARTIDA CORPO ESFERA ALAVANCA EM INOX 304 PASSAGEM PLENA VEDACAO PTFE PN25 (CLASSE 300) ROSCA BSP POL 1/2''	04	PÇ
	77780	A15	NIPLE REDUCAO FG BSP POL 1/2" POL 1/4"	04	PÇ
	30724	A16	LUVA FG BSP POL 1/4"	04	PÇ
	319445	A17	MANOMETRO ANALOGICO ACO INOX 304 CAIXA 50/52MM IP 65 VISOR POLICARBONATO ENCHIMENTO GLICERINA MONTAGEM DIRETA VERTICAL INOX 1000KGF/CM2 BSP 1/4 POL	04	PÇ
	326621	S/N	KIT PARAFUSO PORCA ARRUELA LISA ACO CARBONO ARRUELA VEDACAO FURACAO PN10 NBR 7675 DN50	04	PÇ
**	270350	S/N	TAMPAO FD CLASSE 50 PARA POCO DE VISITA PADRAO SANEPAR	02	PÇ
**	313629	S/N	ESCADA TIPO MARINHEIRO PRFV SEM GAIOLA ALTURA MENOR 3,5M	1,5	m

* VER ESPECIFICAÇÃO TÉCNICA.
** VER ESPECIFICAÇÃO BÁSICA CÓDIGOS SAM.

NOTAS

01 – DIMENSÕES EM CENTIMETROS E ELEVAÇÕES EM METROS, EXCETO ONDE INDICADO.
02 – CONFIRMAR A POSIÇÃO E A PROFUNDIDADE DAS TUBULAÇÕES EXISTENTES NA OBRA.
03 – OS DANOS CAUSADOS ÀS INSTALAÇÕES SUBTERRÂNEAS SERÃO DE INTEIRA RESPONSABILIDADE DA EXECUTORA DAS OBRAS, INDEPENDENTEMENTE DA INTERFERÊNCIA CONSTAR OU NÃO NOS DESENHOS.
04 – CAIXAS DE CAPTAÇÃO E POÇOS DE VISITA PARA GALERIA – EXECUTAR CONFORME MOS 4a EDIÇÃO MÓDULO 15 ITEM 150315 (PÁGINA 08/22).
05 – CONFIRMAR ESPECIFICAÇÕES DOS EQUIPAMENTOS COM OS FORNECEDORES.
06 – QUALQUER ADAPTAÇÃO DEVERÁ SER FEITA PELA CONTRATADA DA OBRA.
07 – O PROJETO BÁSICO HIDRÁULICO FOI COMPATIBILIZADO COM OS DEMAIS PROJETOS CONTRATADOS, CONFORME AS ESPECIALIDADES LISTADAS ABAIXO.

PROJETO/SERVIÇO	DESENVOLVIMENTO
BÁSICO HIDRÁULICO	S.J.M.H. ENGENHARIA E CONSTRUÇÕES LTDA.
TOPOGRAFIA	SOCIEDADE DA ÁGUA SERVIÇOES AMBIENTAIS E GEOTECNOLOGIAS
BÁSICO ELÉTRICO/AUTOMAÇÃO	S.J.M.H. ENGENHARIA E CONSTRUÇÕES LTDA.
BÁSICO MECÂNICO/ESPECIFICAÇÕES	S.J.M.H. ENGENHARIA E CONSTRUÇÕES LTDA.
SONDAGENS SPT	GEOLOC LOCAÇÕES E SONDAGENS LTDA.
BÁSICO ESTRUTURAL	S.J.M.H. ENGENHARIA E CONSTRUÇÕES LTDA.
BÁSICO GEOTÉCNICO	S.J.M.H. ENGENHARIA E CONSTRUÇÕES LTDA.

SANEPAR Companhia de Saneamento do Paraná

MUNICÍPIO/SISTEMA:
GENERAL CARNEIRO - JANGADA DO SUL
SISTEMA DE ABASTECIMENTO DE ÁGUA

BLOCO Nº: FOLHA Nº:
01 - 08/09

PROJETO/UNIDADE CONSTRUTIVA:
PROJETO BÁSICO HIDRÁULICO
VÁLVULA REDUTORA DE PRESSÃO - DN50 (2")
PLANTA, CORTE E DETALHE

DATA: AGOSTO/2023

ESCALA: INDICADA

GERÊNCIA DA SANEPAR:
GPOSD
Gerência Projetos e Obras Sudeste
R. Monte Alverne nº644 - Jardim Carvalho - CEP 84016-010 - Ponta Grossa - PR
GERENTE: JOEL PIRES CREA Nº: 100.276 - D/PR

COORDENADOR GERAL DO PROJETO: DENIS SCHECHTEL NEVES CRQ 09402617/PR	FISCALIZAÇÃO DO PROJ. ELÉTRICO E AUTOM.: -
FISCALIZAÇÃO DO PROJETO CIVIL/HIDRÁULICO: DIOGENES VERGES 78.132 - D/PR	FISCALIZAÇÃO DO PROJ. UNIDADES LINEARES: -
FISCALIZAÇÃO PROJ. ESTRUT., GEOTEC. SOND.: DIOGENES VERGES 78.132 - D/PR	DESENVOLVIMENTO DO DESENHO: -
FISCALIZAÇÃO DO PROJETO MECÂNICO: ARTHUR VIEIRA NETO 107.842 - D/PR	ADEQUAÇÃO DO DESENHO: -

EMPRESA CONTRATADA
SJMH
S.J.M.H. Engenharia e Construçoes Ltda.
R. Marechal Deodoro nº530, Sala 104 - CEP 80010-010 - Curitiba-PR - e-mail: sjmh@sjmh.com.br

RESP. TÉCNICO DO PROJETO: SONG JON SCREMIN	RESP. TÉCNICO DO PROJETO: ---
CREA Nº: 166.833 - D/PR	CREA Nº: --
ARQUIVO ELETRÔNICO: 008-SAA-0674-9142-PBHI-DE-0000VRP01DETALHAMENTO-R0	